

POR TAF OLIO

Manoukian Alan Thomas



Manoukian Alan Thomas

Soy estudiante avanzado de la carrera de Arquitectura en la FADU, Facultad de Arquitectura, diseño y urbanismo, en Buenos Aires, Argentina.

Me considero una persona abierta a nuevas experiencias y profundamente dedicada a los proyectos, con el objetivo de crear espacios que generen un impacto positivo en las personas, donde puedan experimentar emociones gratificantes y transformadoras.

Tengo muchas ganas de participar en proyectos colaborativos con referentes profesionales, donde pueda aplicar los conocimientos adquiridos y seguir aprendiendo para generar nuevas experiencias.

thomasmanoukian1118@gmail.com
+54 9 11 3872-3400

formación

2020 - 2026 **Facultad de Arquitectura, Diseño y Urbanismo**
Tercer año de la carrera de arquitectura.

2020 - 2021 **Curso de programación #YoPrograma**
Certificado en Full Stack Junior. Desarrollo de habilidades para la programación de páginas webs.

2014 - 2020 **Secundaria tecnica ORT Almagro**
Titulación en bachillerato en Artes Visuales con especializacion en Construcciones y Dineño. Graduado con honores.

habilidades

Modeling	SketchUp | Revit
Drawings	AutoCAD
Rendering	Endscape | Twinmotion | D5 render
Soft Skills	Paquete Office | Adaptabilidad | Creatividad
Adobe Pack	Adobe Photoshop | Adobe Illustrator | Adobe Premier

logros personales

(2019 - 2020) 1ºer lugar en el concurso EFIcasa, desarrollo de un stand para un evento.
(2014 - 2020) Invitación a viajes estudiantiles, Londres y Puerto Madryn, por merito de calificaciones.
(2008 - 2020) Participación en torneos de natación municipales, nacionales e interescolares.

idiomas

Inglés	Nivel B1 (Avanzado)
Español	Nativo
Armenio	Básico

indice.

01



TATWERS

02



CASA NUÑEZ

03




MITOSIS

04



CLINICA

05

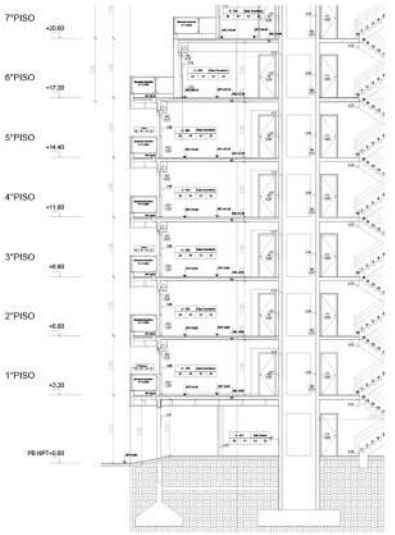

DOCUMENTACIÓN

TATWERS

"Díseño que conecta, comunidad que proyecta"

Este proyecto es nuestra respuesta a un contexto urbano como el de la ciudad de Buenos Aires, donde la densidad de la población aumenta y el suelo disponible es cada vez más escaso, por lo que intentamos promover la inclusión y el bienestar de una población diversa.

Se plantea una nueva forma de utilizar los lotes para mejorar el vecindario a través de una densificación consciente utilizando edificios de pequeña superficie para actividades residenciales y comerciales. Organizádose para crear más espacios comunitarios y verdes. Se trata de un enfoque que promueve un desarrollo urbano equilibrado, no excesivo.

El proyecto es nuestro modelo para una comunidad de convivencia compartida para personas tanto mayores, como para jóvenes trabajadores. El objetivo es permitir una mejor vida cotidiana a través de los beneficios de una comunidadunida con acceso a instalaciones y servicios compartidos, creando ambientes donde los vecinos se conozcan y compartan estos recursos.


Tipologia de unidad 1
usuario nomade digital
m2 35m2
1 nivel- monoambiente
cant de unidades 3






Tipologia de unidad 2
usuario nomade digital
m2 70m2
2 niveles- 2 ambientes
cant de unidades 16



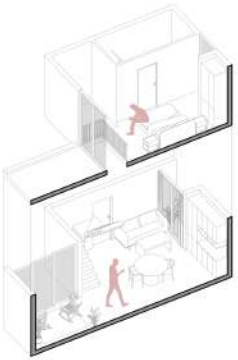

Tipologia de unidad 3
usuario adultos mayores
m2 60m2
1 nivel- 2 ambientes
cant de unidades 9




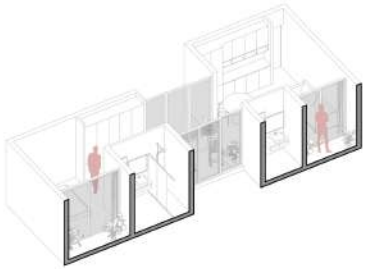







01 tatwers

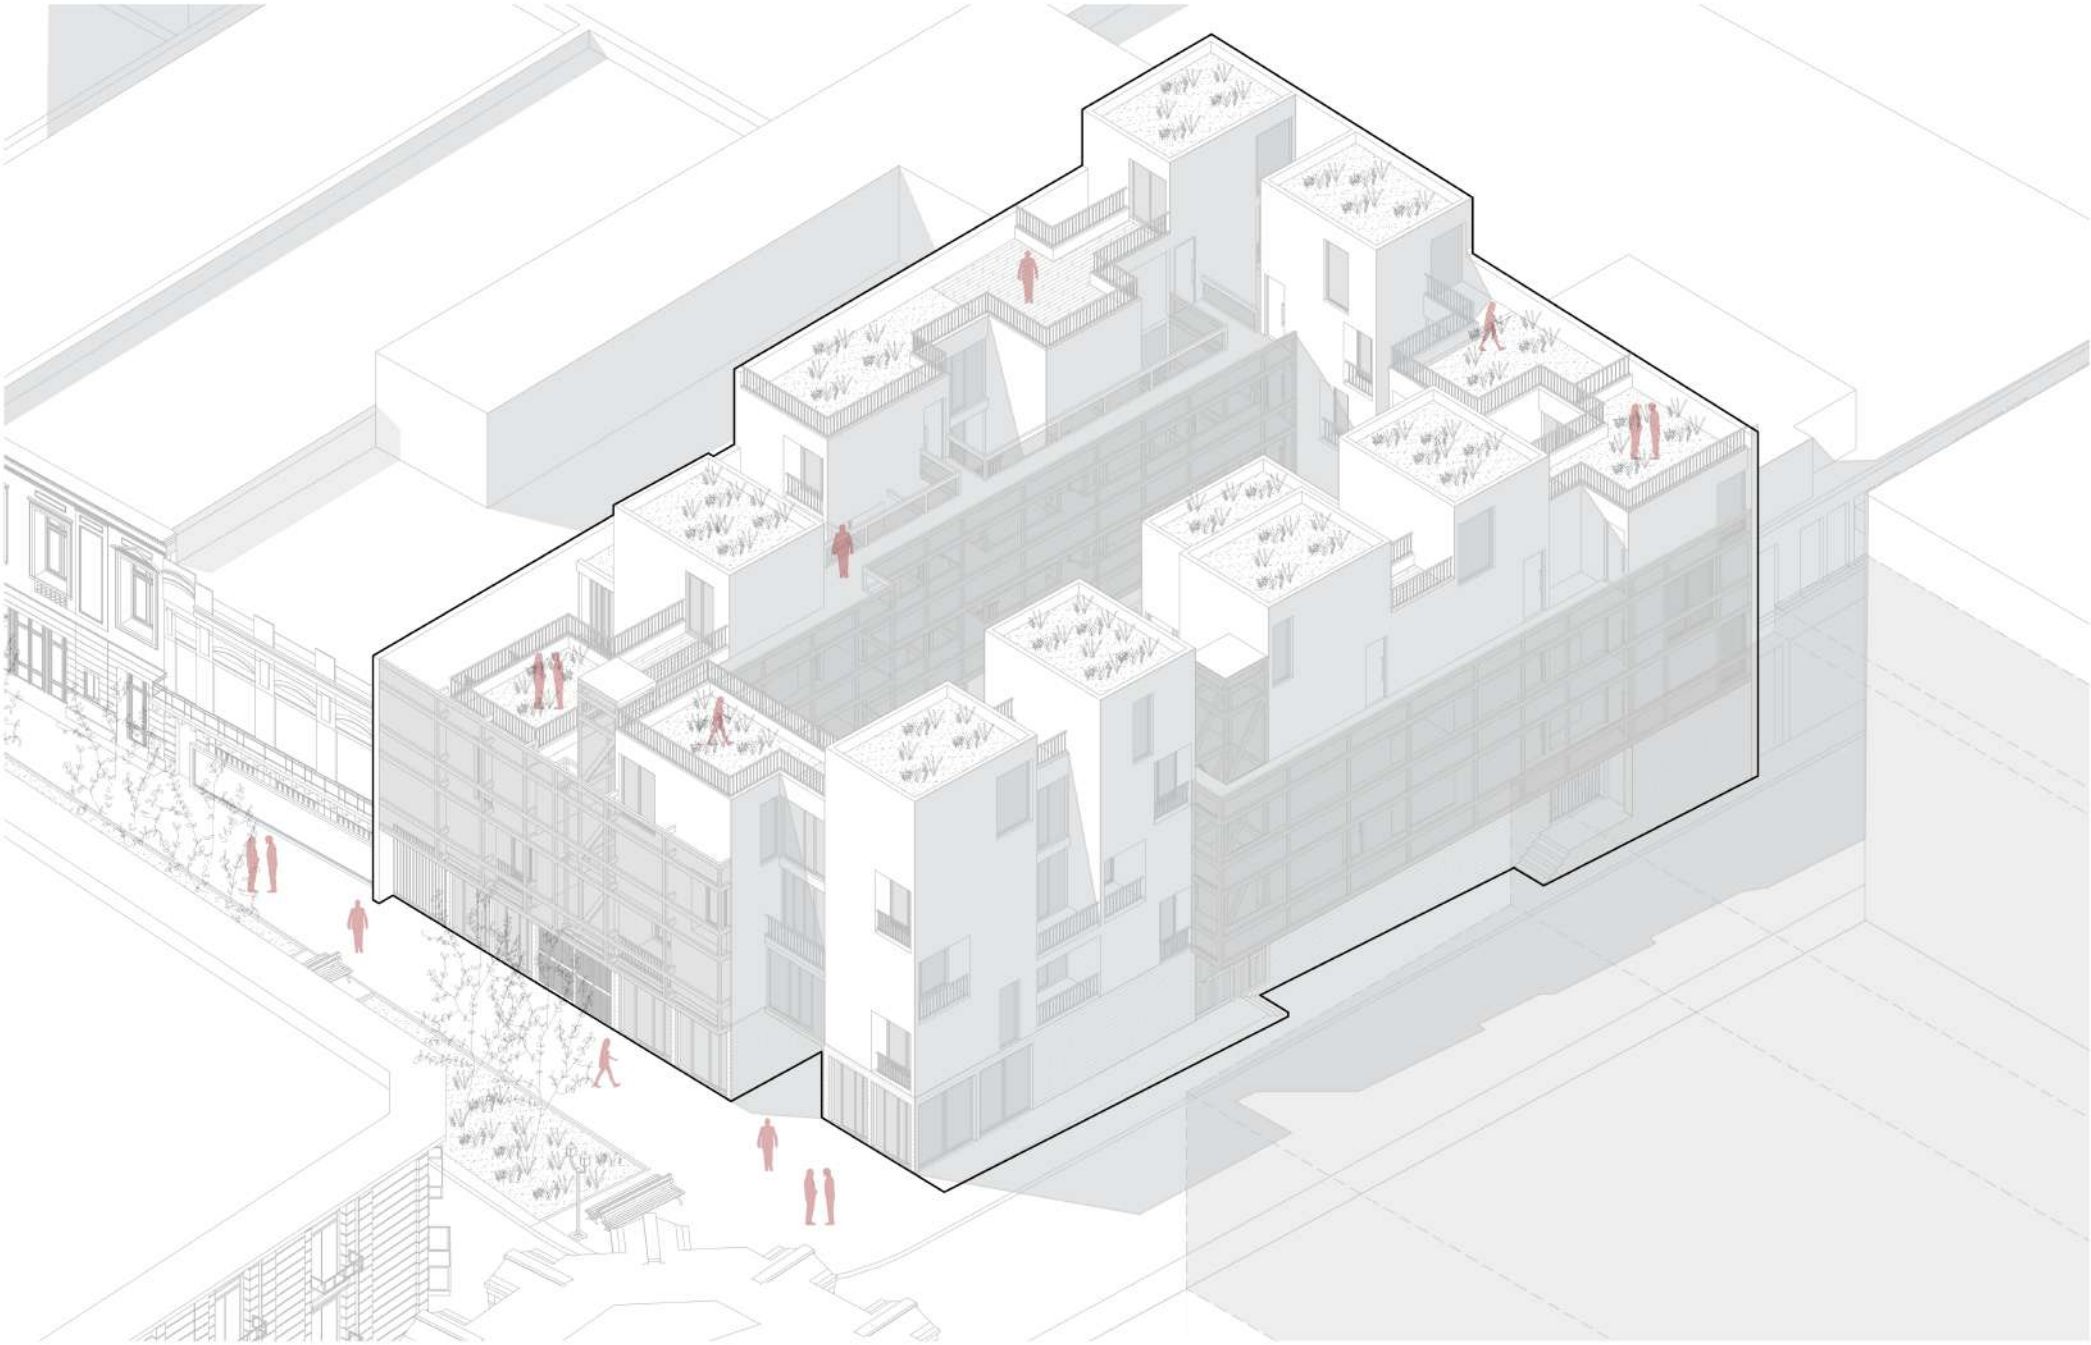

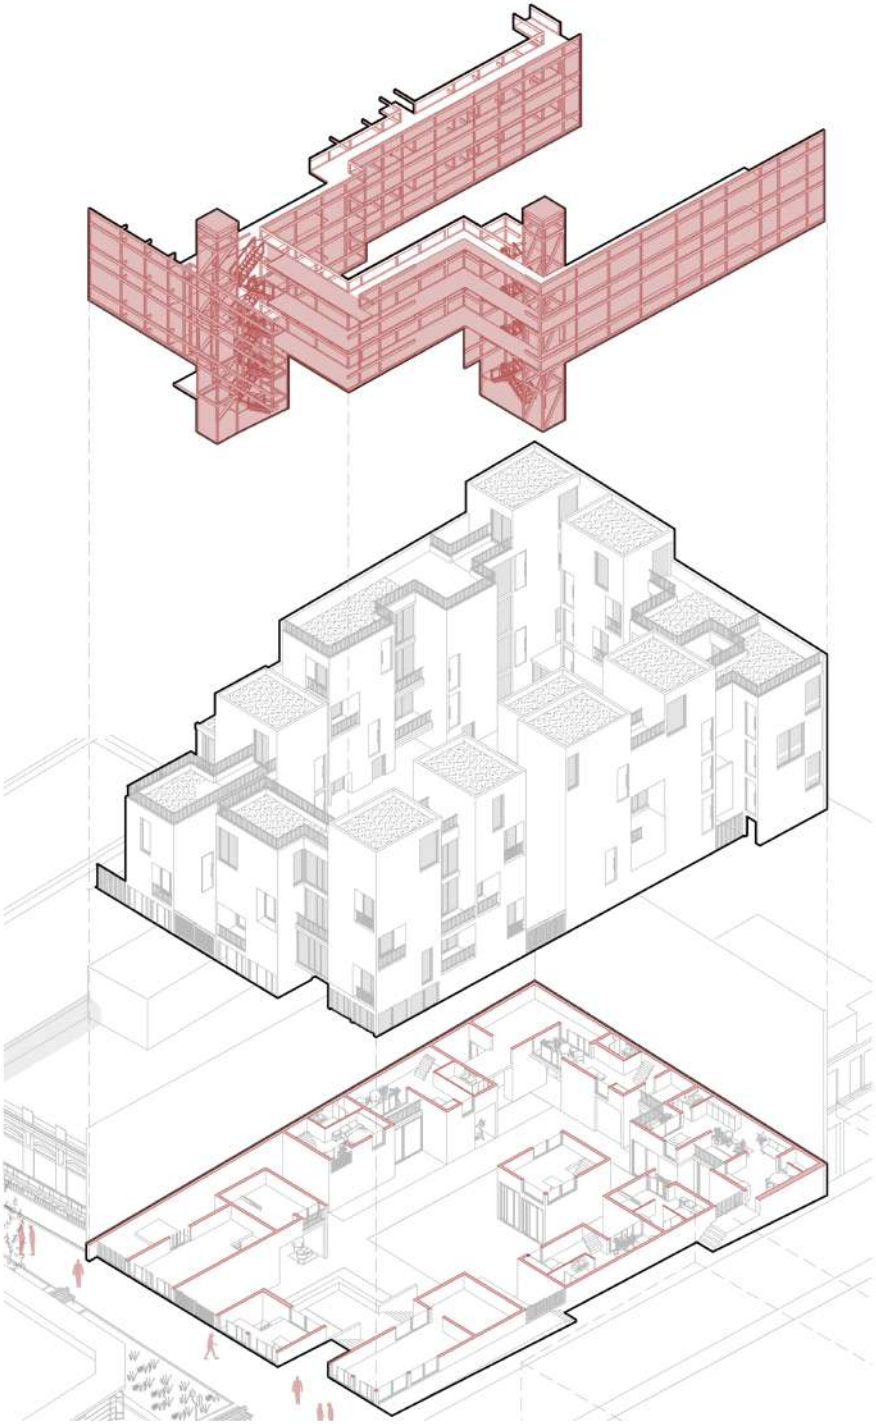





UTILIDADES

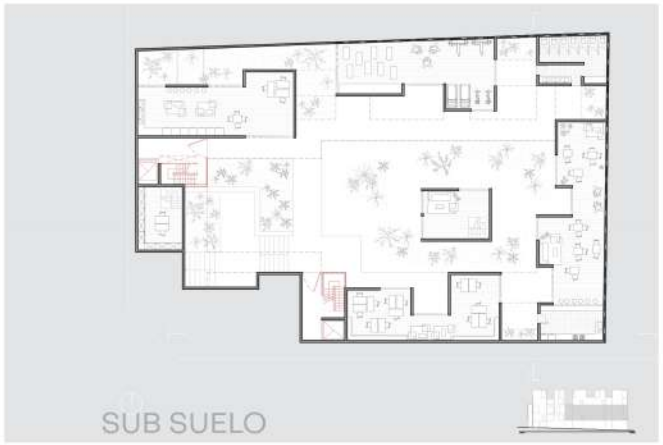

SUB SUELO



Balcarce
PRIMERA PLANTA
Venezuela


Balcarce
PLANTA BAJA
Venezuela

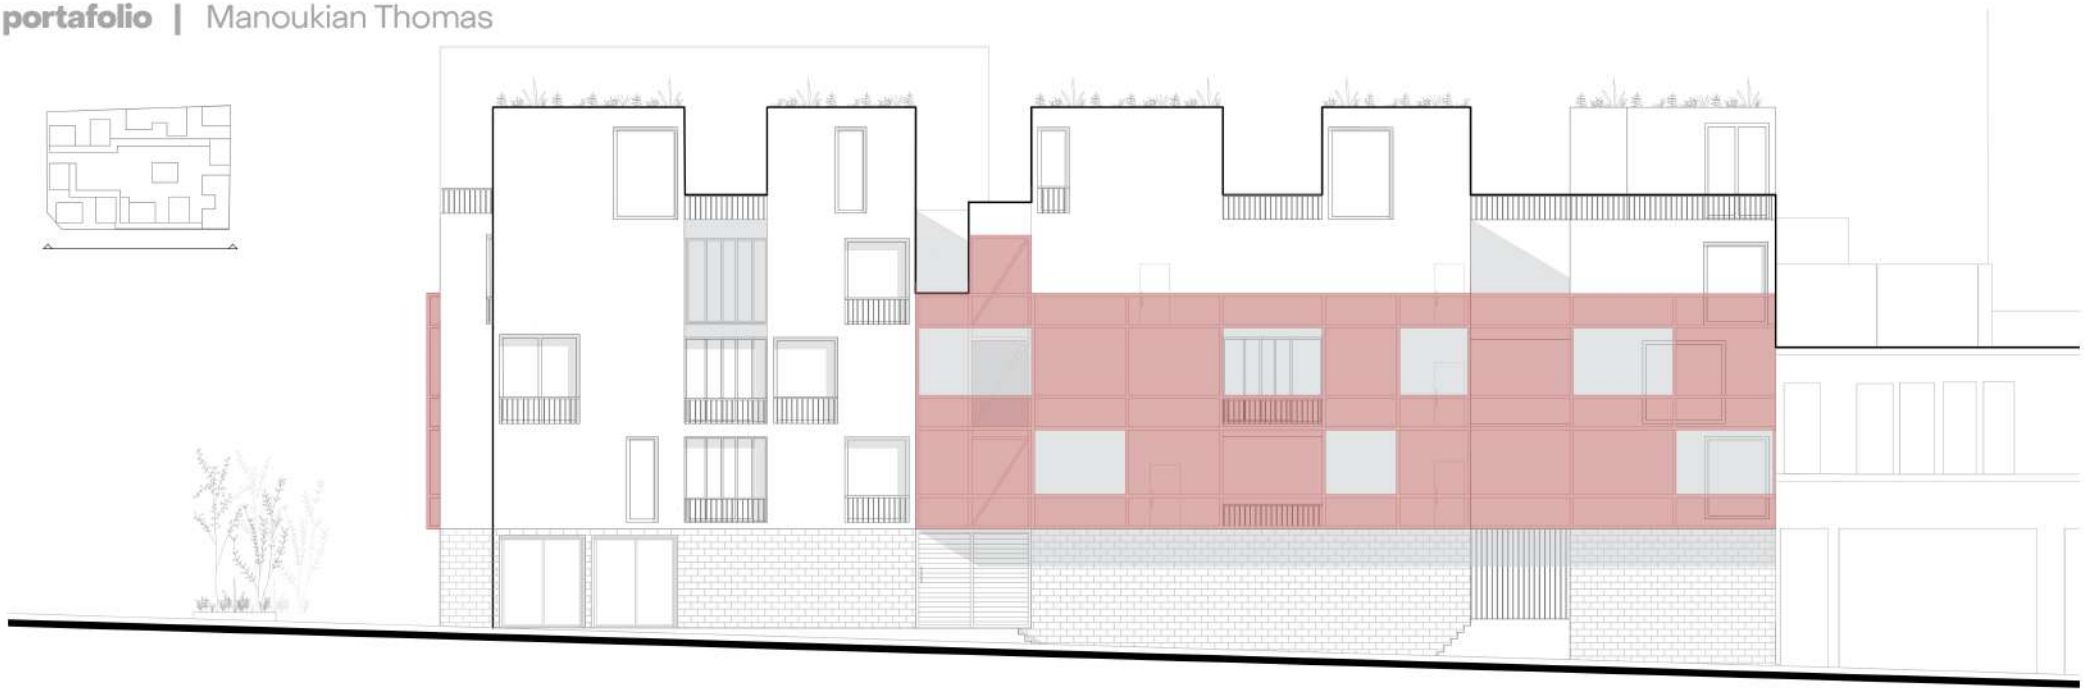


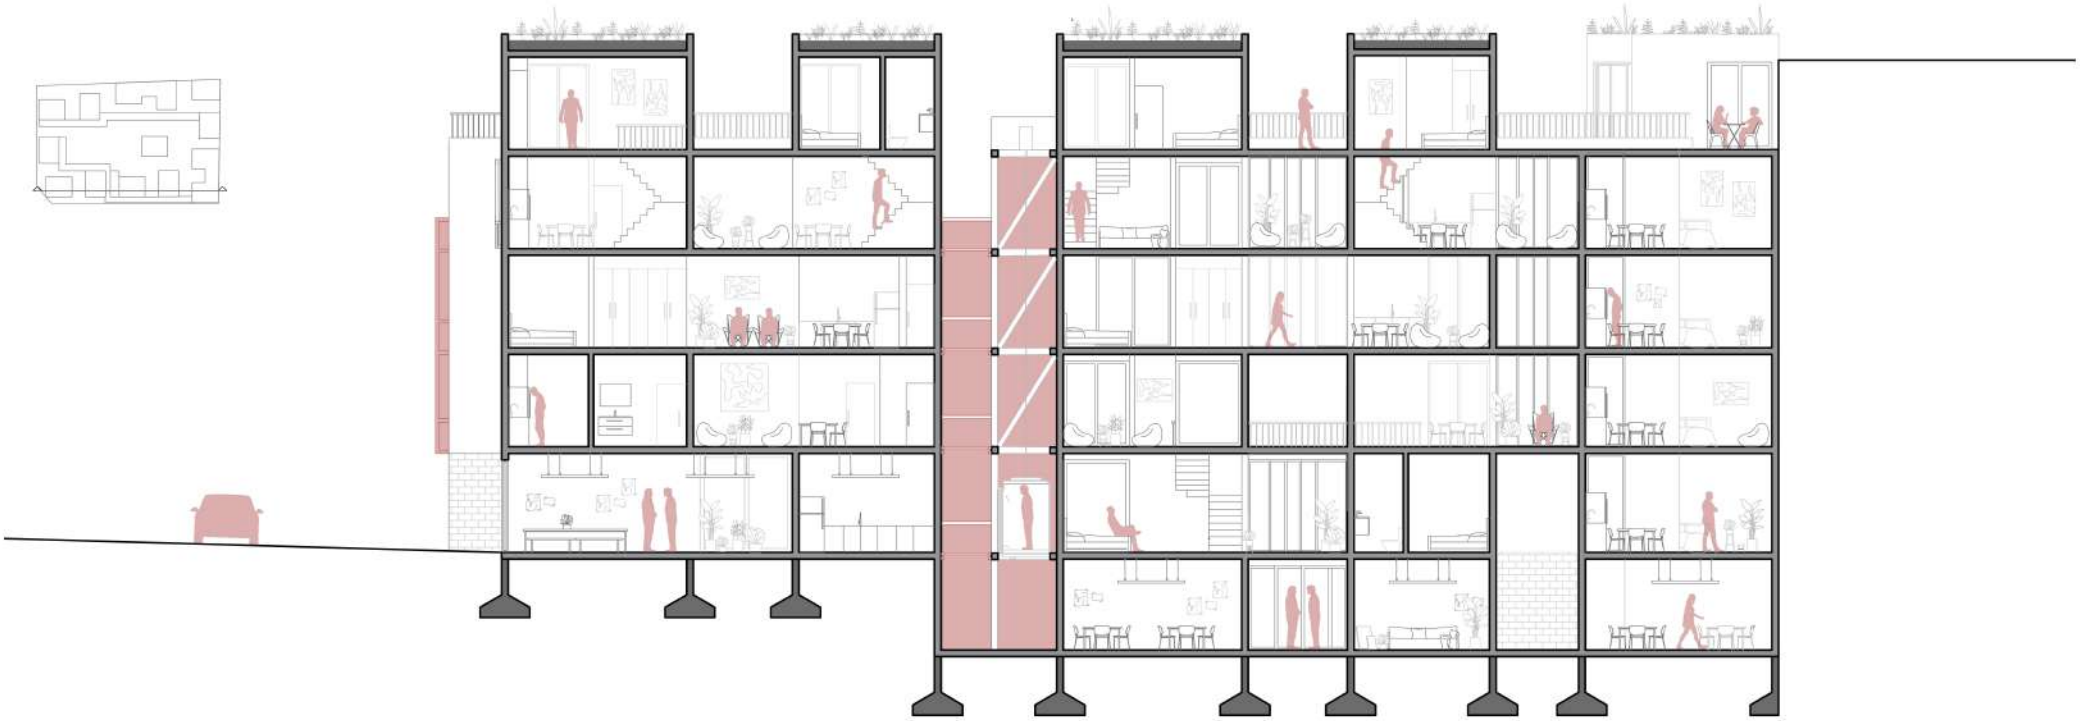


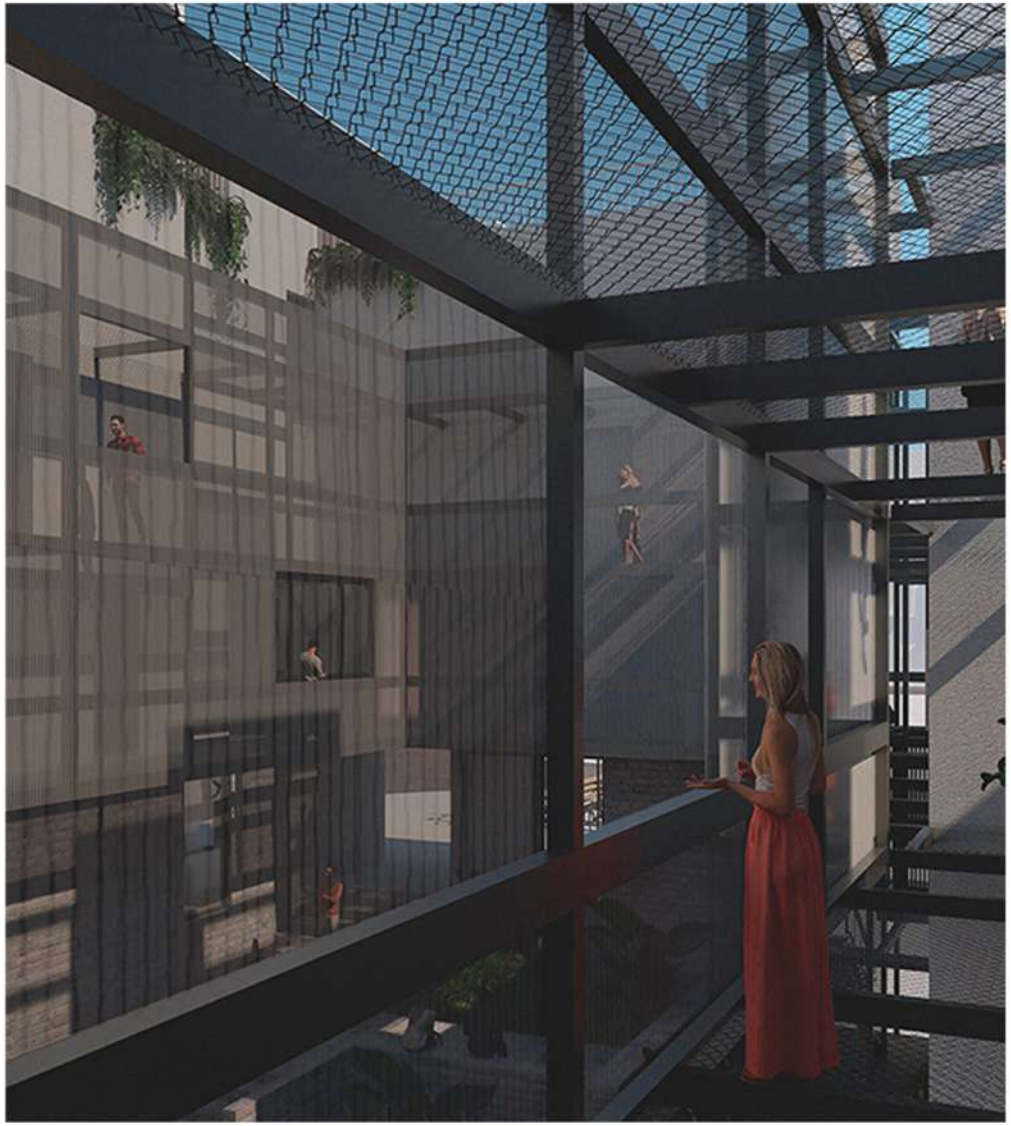

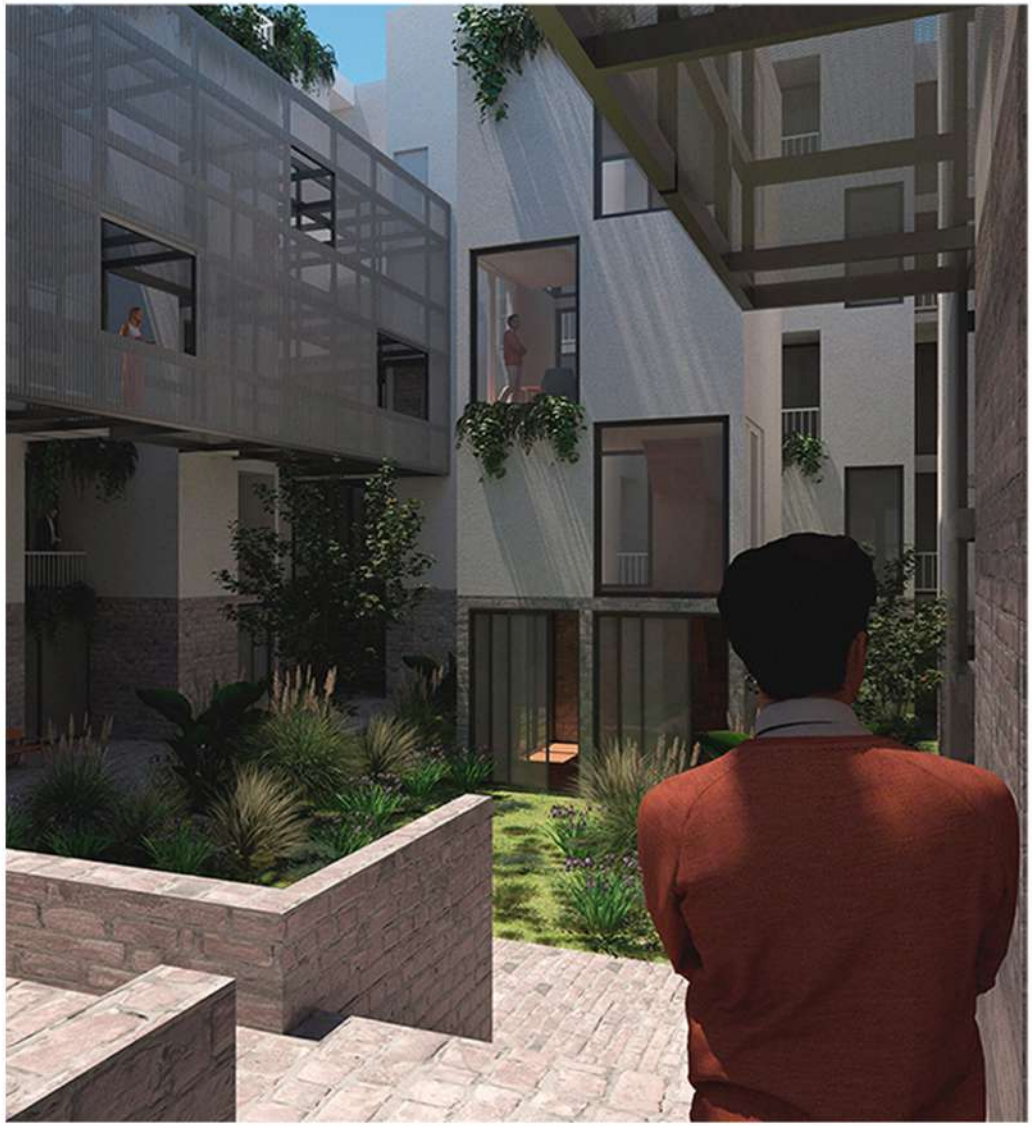



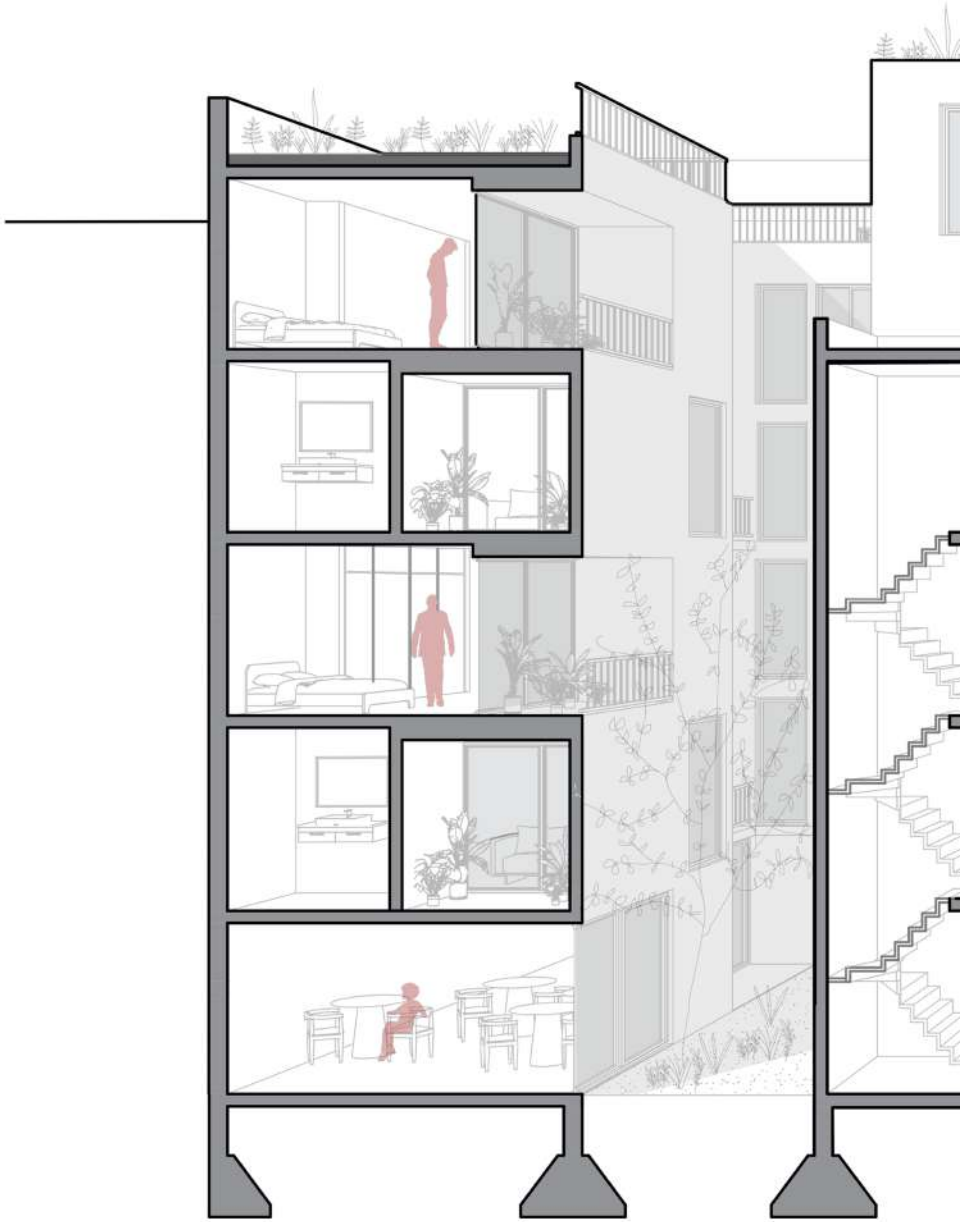

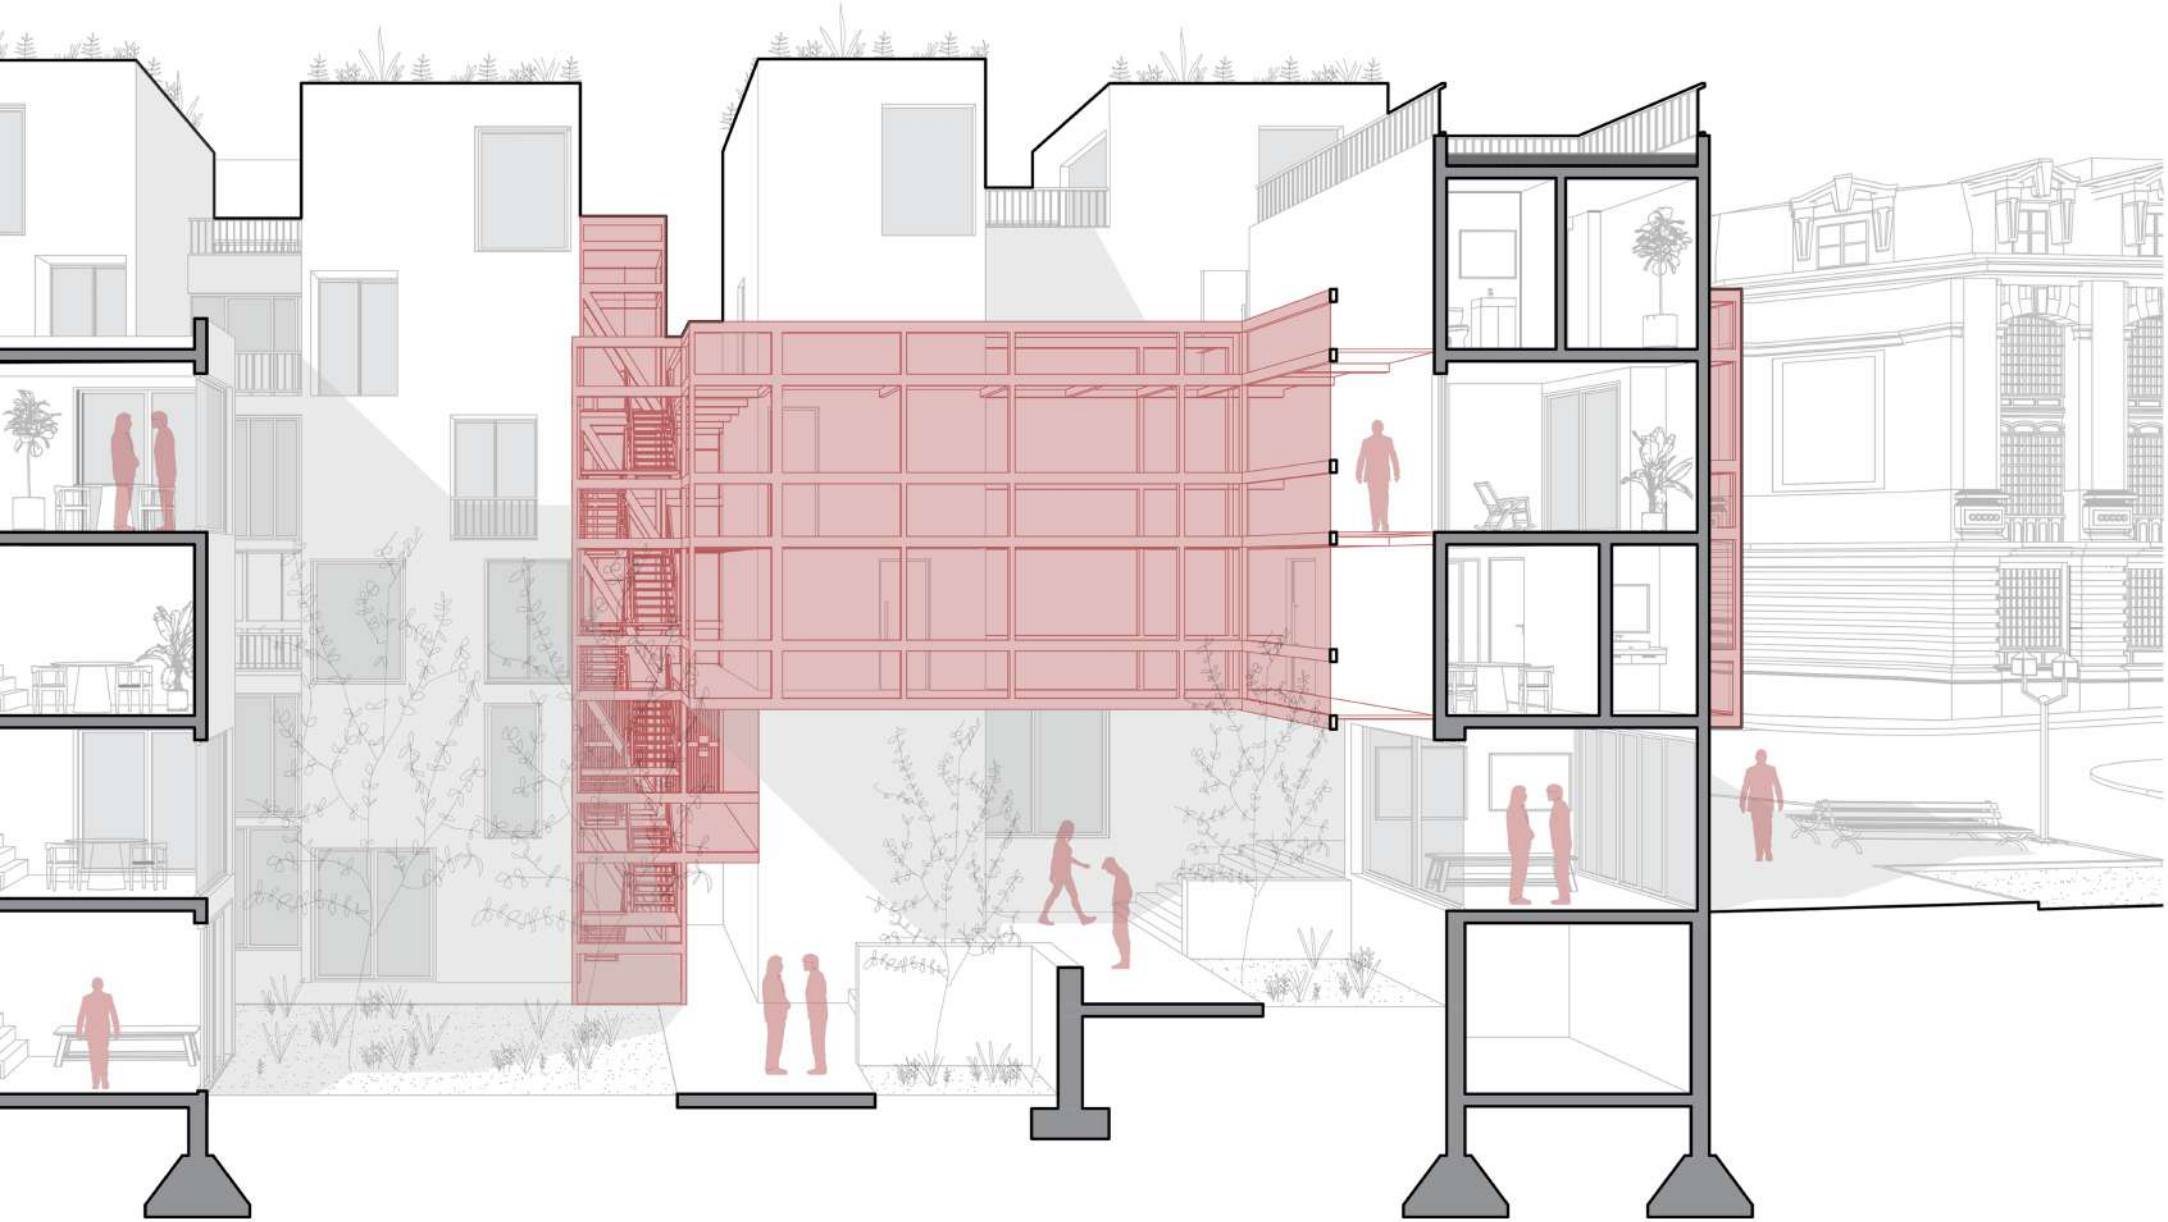


CASA NUNEZ

"Tres prismas, un equilibrio: donde trabajo y hogar se encuentran."


A la hora de diseñar este proyecto, se pensó cuidadosamente en el tipo de cliente al que se adaptarán los diferentes espacios de la casa. Este proyecto está especialmente dirigido a personas que trabajan desde casa, una necesidad cada vez más común en el entorno actual. En este sentido, el diseño busca optimizar el espacio para combinar la vida laboral y personal de manera eficiente.

Para ello, se desarrolló un concepto arquitectónico basado en tres prismas simples que se intercalan entre sí. Cada uno de estos prismas tiene una función específica dentro de la distribución de la casa, lo que permite una organización clara y funcional de los espacios.


El primer prisma alberga los espacios públicos, el segundo prisma corresponde a los espacios más privados de la casa, miestras que en el tercer y ultimo prisma se encuentran la zona de estudio y la recámara principal.

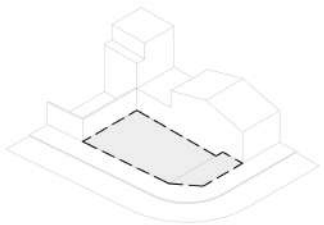


01 SITIO

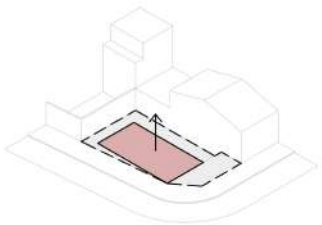


02 MODULO

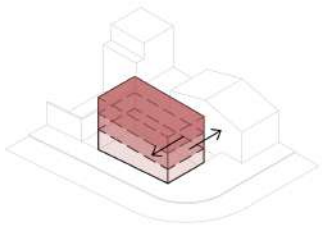


03 NIVELACIÓN

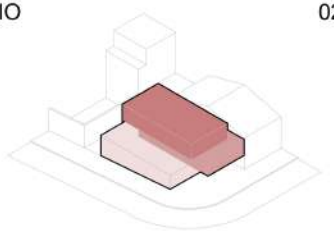

04 DISTRIBUCIÓN

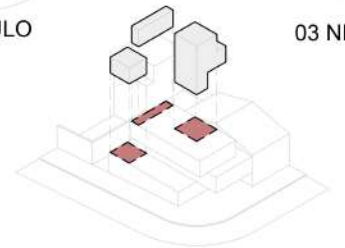


05 EXTRACCIÓN

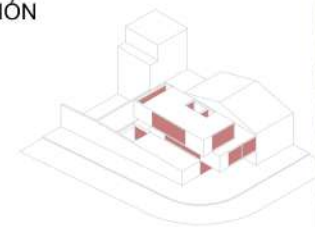



06 CARPINTERIAS




02 casa nunez

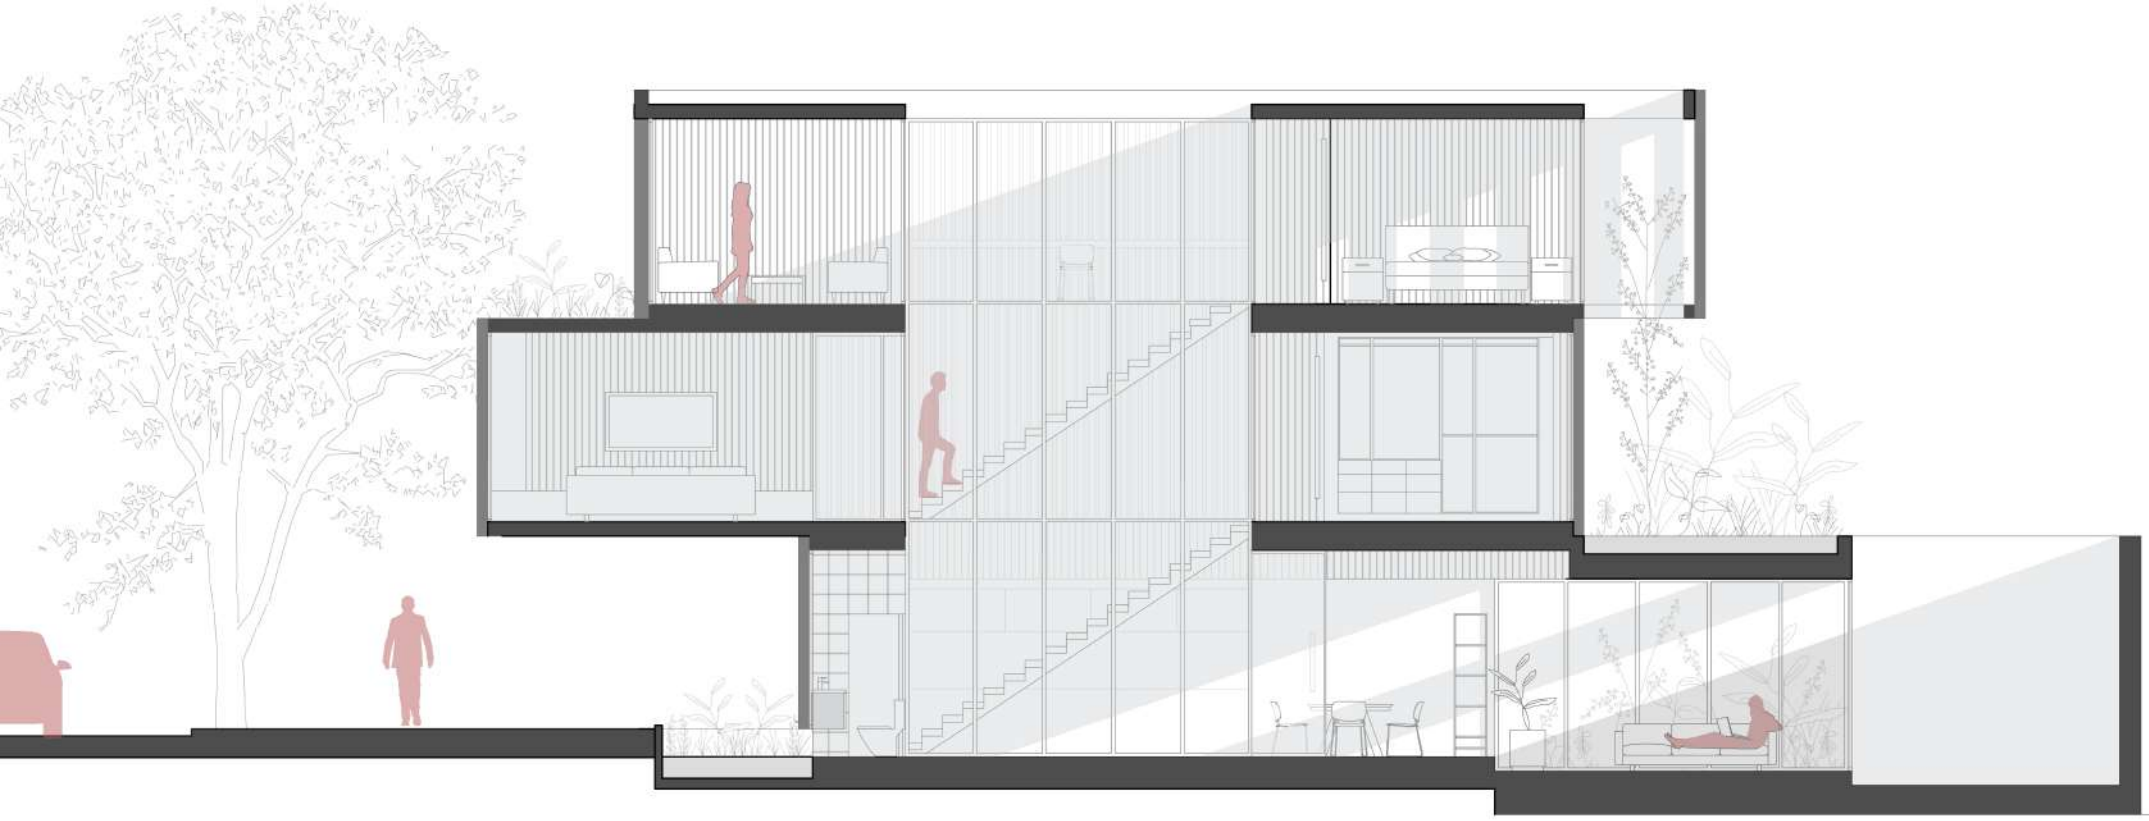

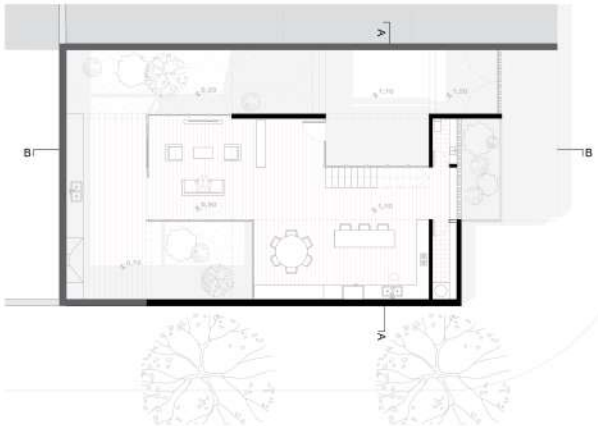
A
B
B
A

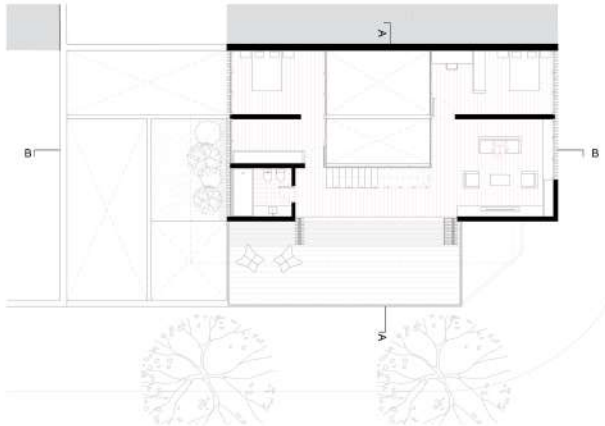
A
B
B
A

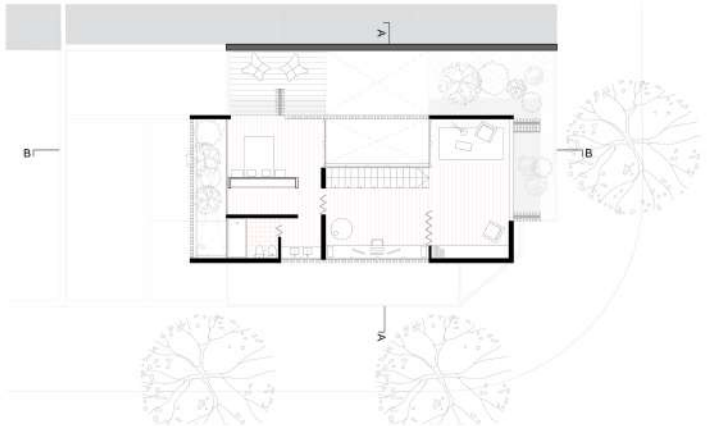

A
B
B
A









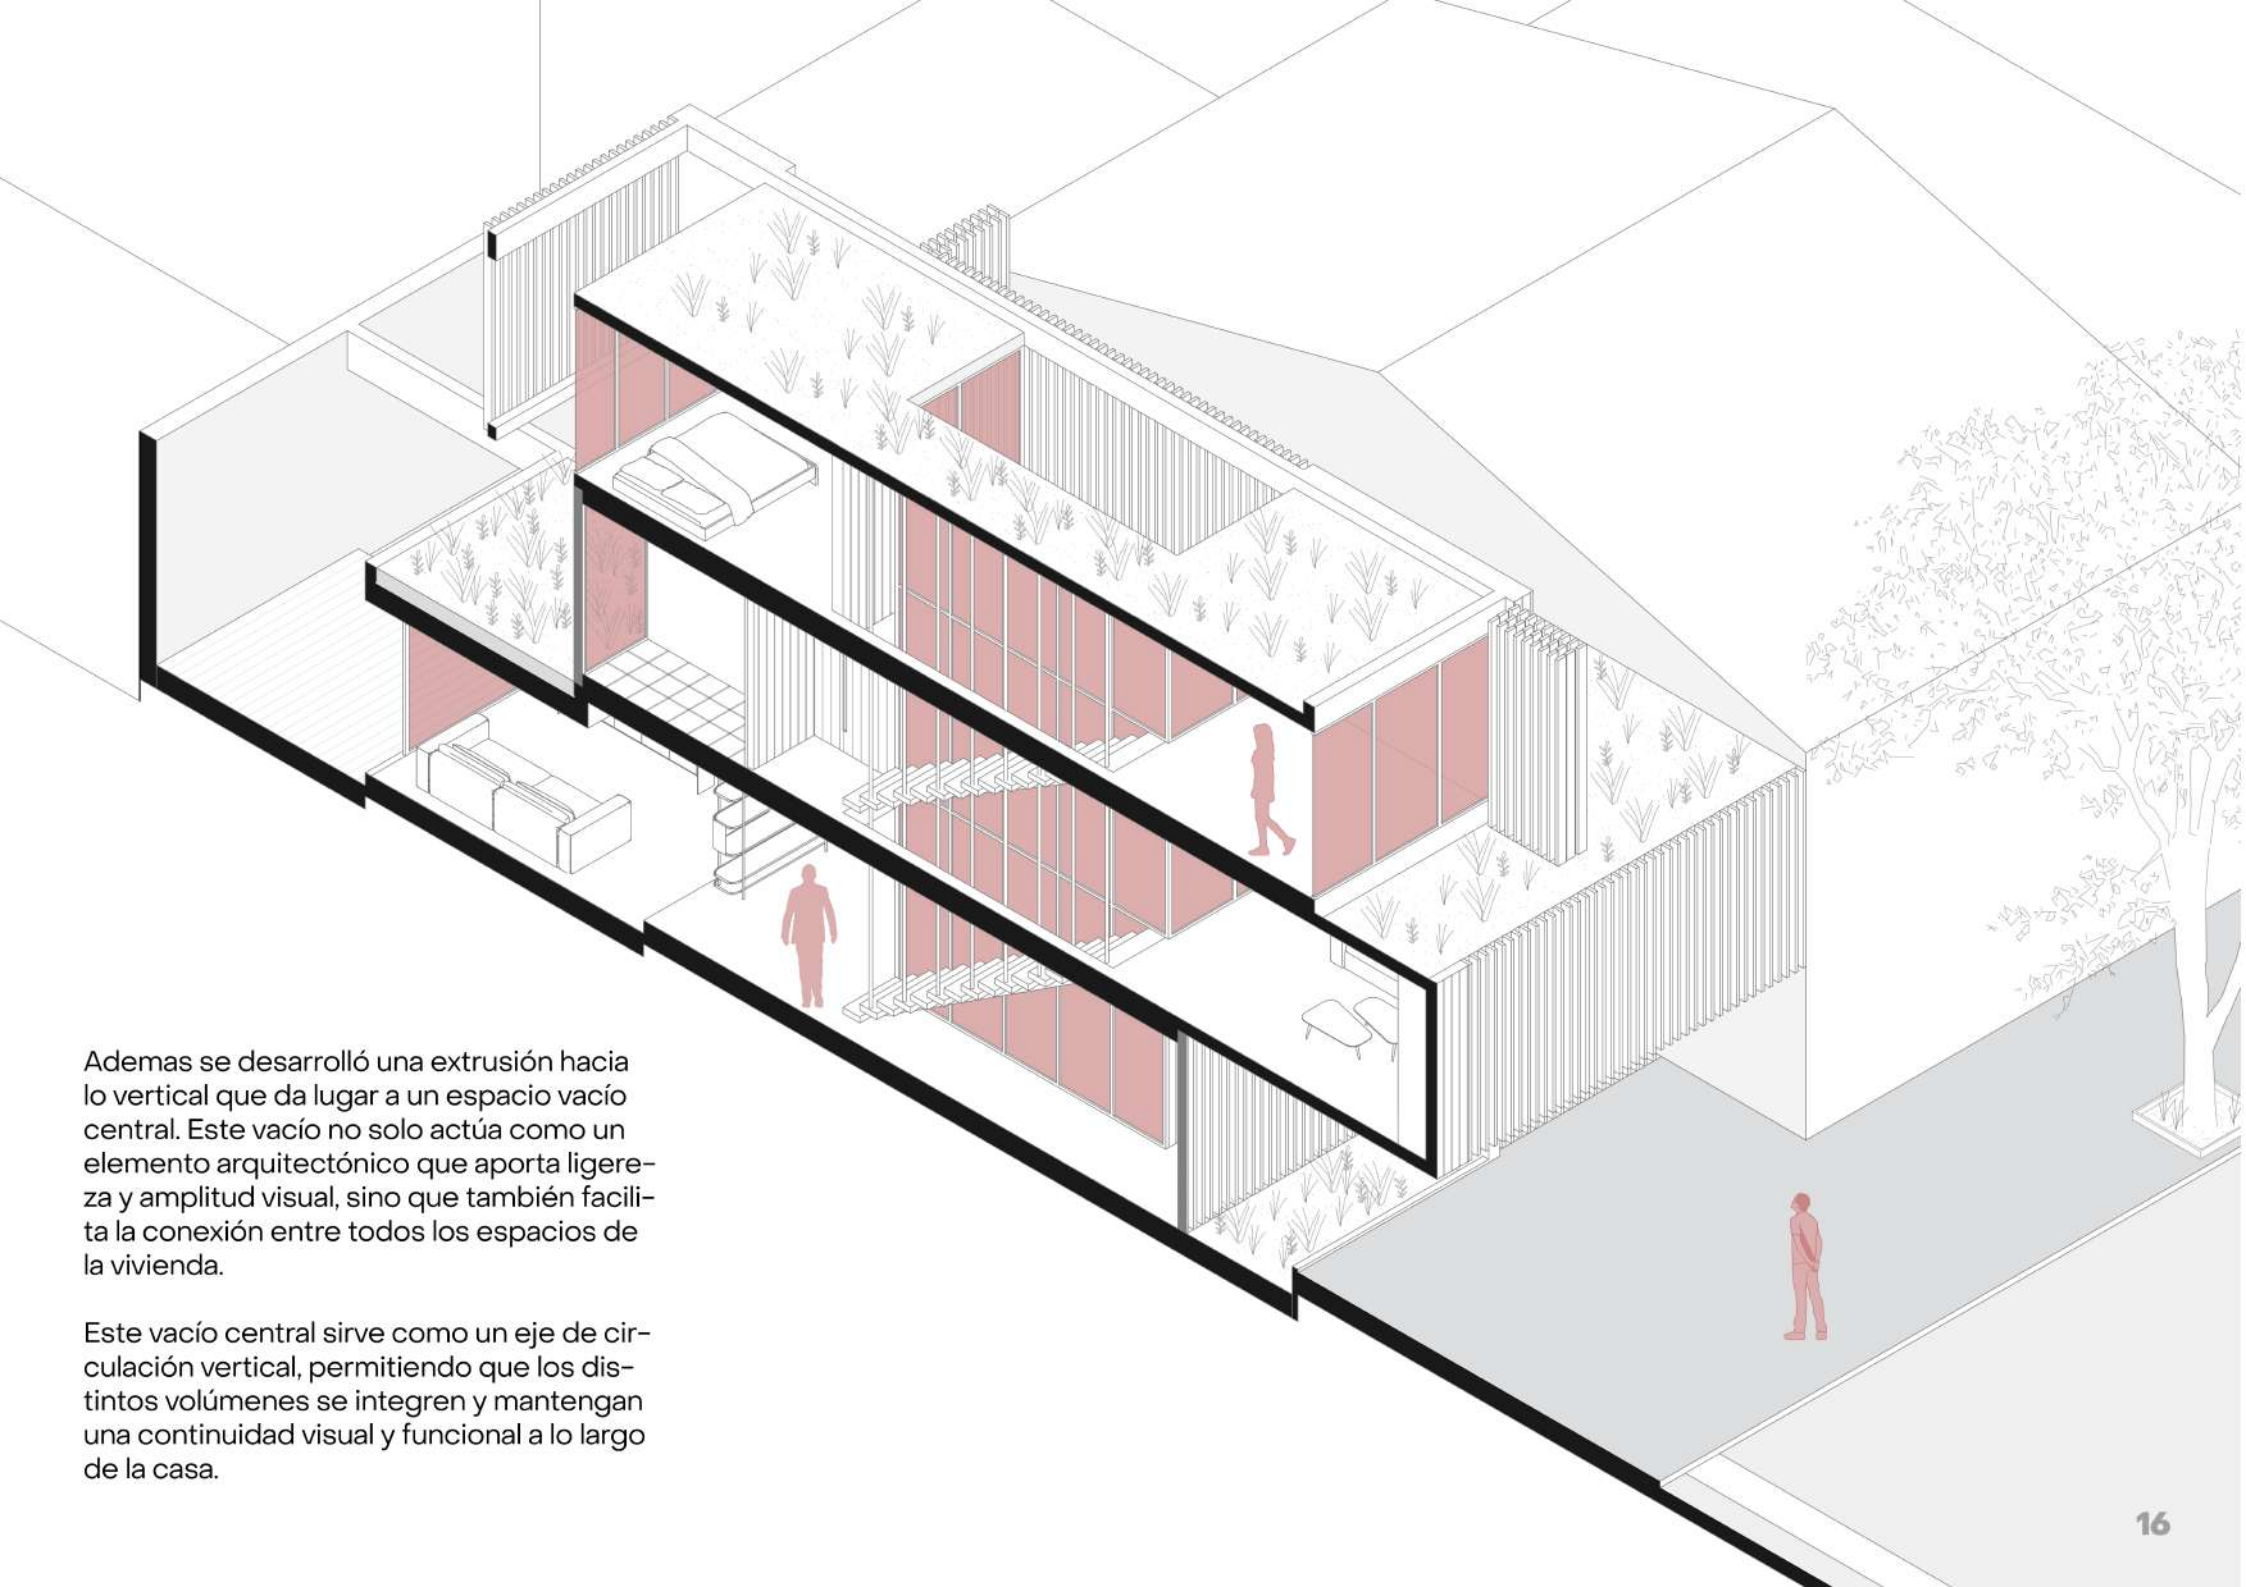

Ademas se desarrolló una extrusión hacia lo vertical que da lugar a un espacio vacío central. Este vacío no solo actúa como un elemento arquitectónico que aporta ligereza y amplitud visual, sino que también facilita la conexión entre todos los espacios de la vivienda.


Este vacío central sirve como un eje de circulación vertical, permitiendo que los distintos volúmenes se integren y mantengan una continuidad visual y funcional a lo largo de la casa.

CLINICA TRAUMATOLOGICA


El proyecto se implanta en un terreno irregular del barrio de Palermo, en un contexto urbano de alta densidad edilicia y escasez de espacios verdes accesibles. Frente a esta condición, se propone liberar la planta baja y destinarla a un espacio verde público que vincula la clínica con el entorno y promueve el bienestar de los usuarios.

El edificio se organiza a partir de un volumen rectangular elevado, sostenido por dos núcleos estructurales verticales, lo que permite generar una planta baja completamente libre y permeable, concebida como una plaza de acceso con usos flexibles como cafetería y áreas de espera.


La barra elevada concentra el programa repetitivo de la clínica, organizado de forma clara y eficiente, con buena iluminación natural, ventilación cruzada y una modulación estructural regular que optimiza la construcción y permite flexibilidad futura. Así, la clínica se integra al tejido urbano como un espacio de salud abierto y accesible para la comunidad.

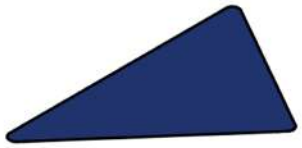


IMPLANTACIÓN
Analisis de la utilización de terreno irregular

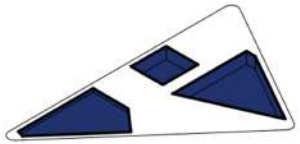


SUBSUELO
Programa ubicado en el subsuelo con la intención de dejar espacio libre en la PB

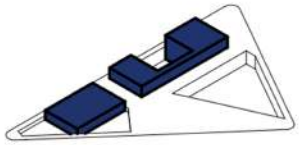

PLANTA LIBRE
Adaptación de la planta baja al entorno sedendo gran espacio a lo publco

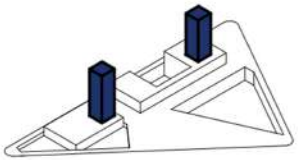

NUCLEOS VERTICALES
Ubicación en puntos estrategicos en la PB

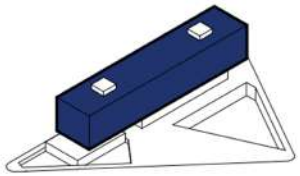


PROGRAMA REPETITVO
Se resuelve en un volumen rectangular exento





03 clinica

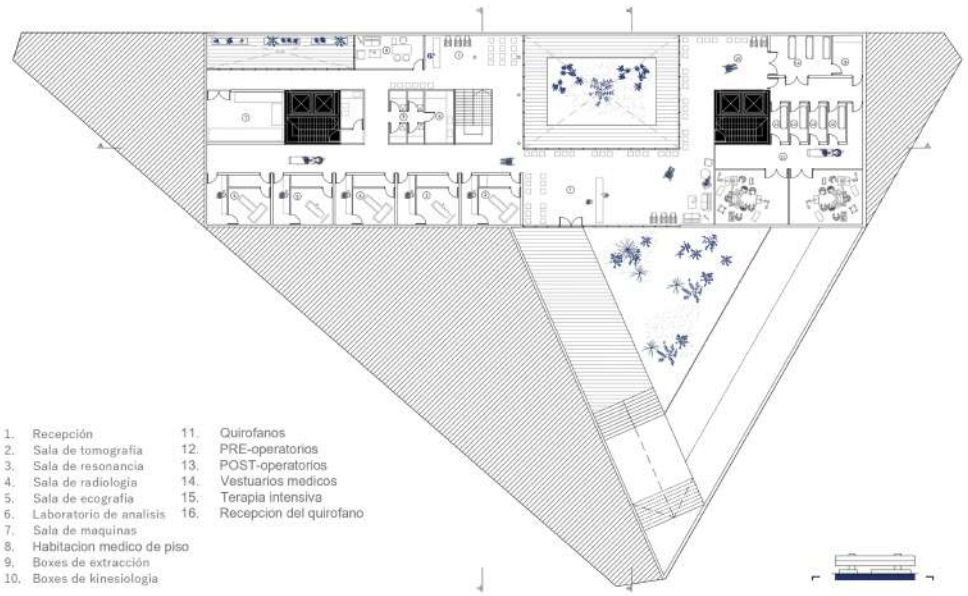



1. Recepción
2. Sala de tomografia
3. Sala de resonancia
4. Sala de radiologia
5. Sala de ecografia
6. Laboratorio de analisis
7. Sala de maquinas
8. Habitacion medico de piso
9. Boxes de extracción
10. Boxes de kinesiologia
11. Quirofanos
12. PRE-operatorios
13. POST-operatorios
14. Vestuarios medicos
15. Terapia intensiva
16. Recepcion del quirofano




1. Recepción
2. Administración
3. Recepción de insumos
4. Cafeteria

Vista A-A

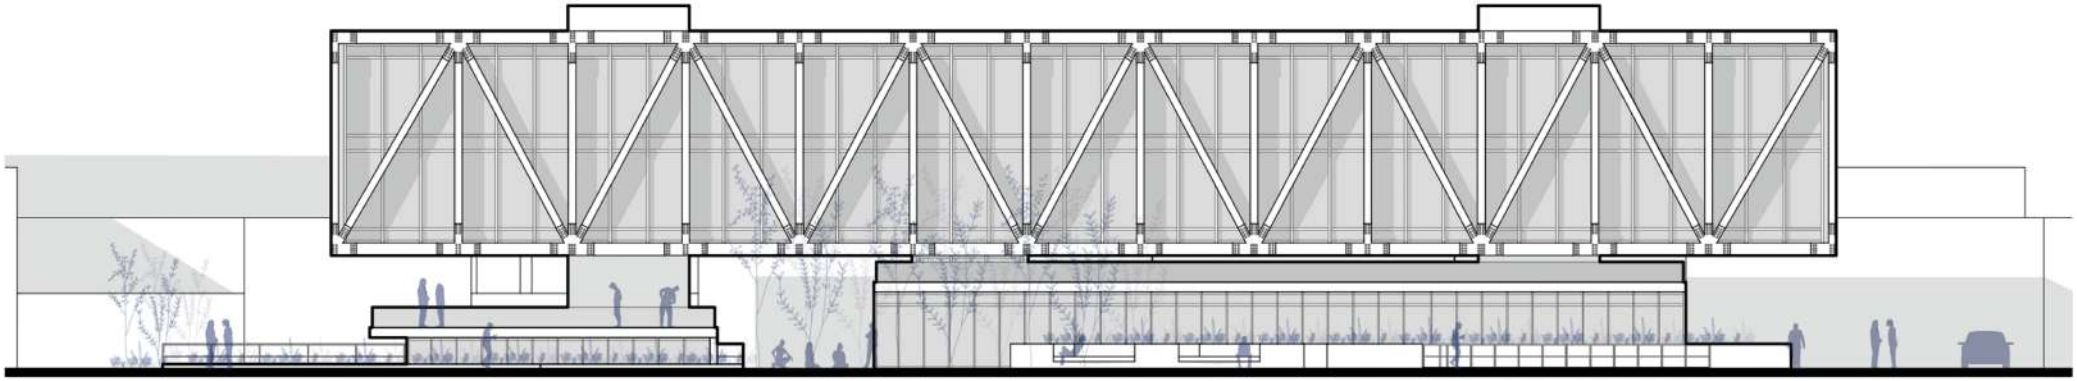


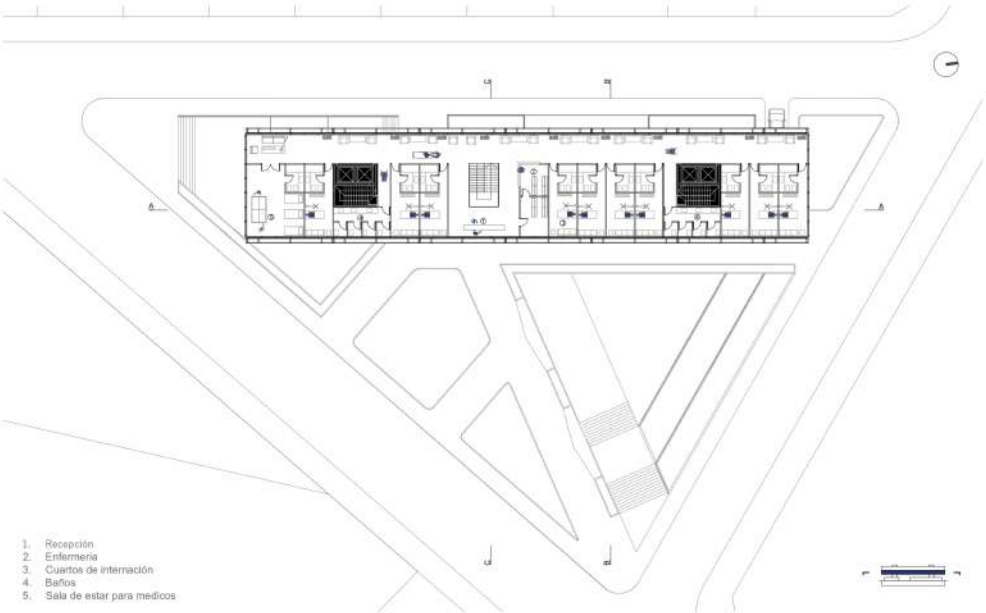


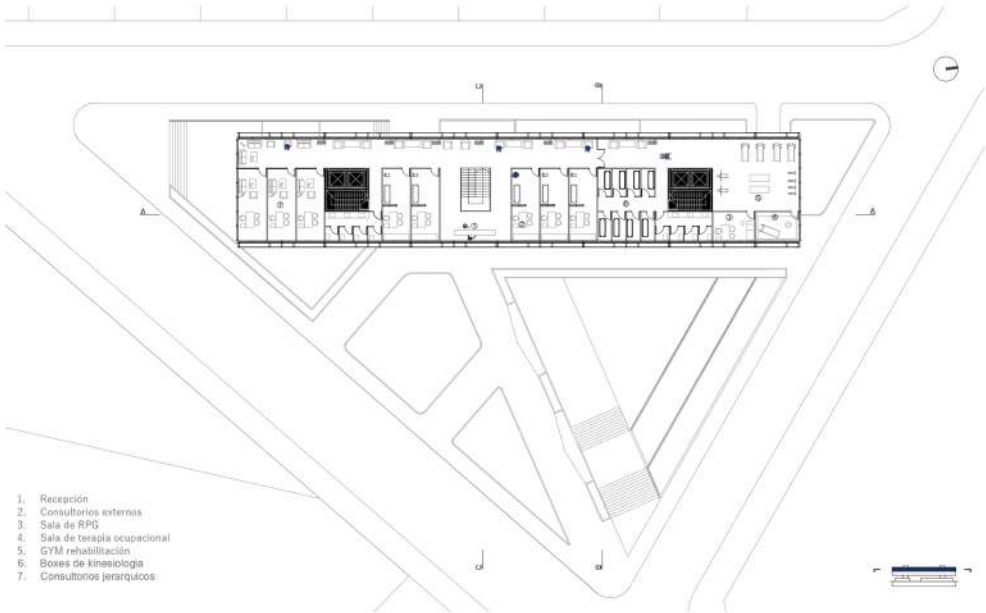



Corte A-A

1. Area consultorios jerarquicos
2. Area consultorios externos
3. Area consultorios de internacion
4. Area medica
5. Cafeteria
6. Hall principal
7. Area administrativa
8. Area de diagnostico
9. Area quirurgica
10. Area de rehabilitación

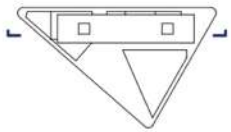


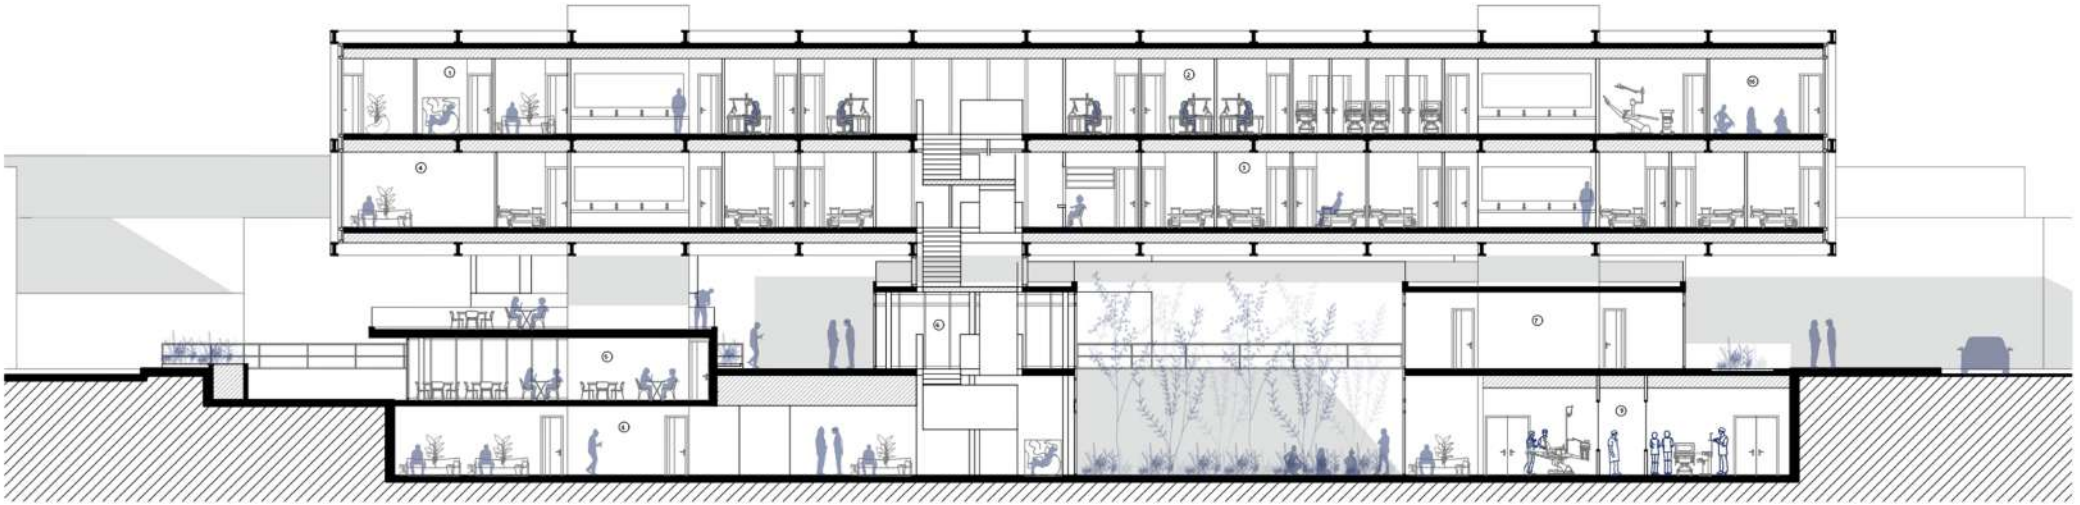

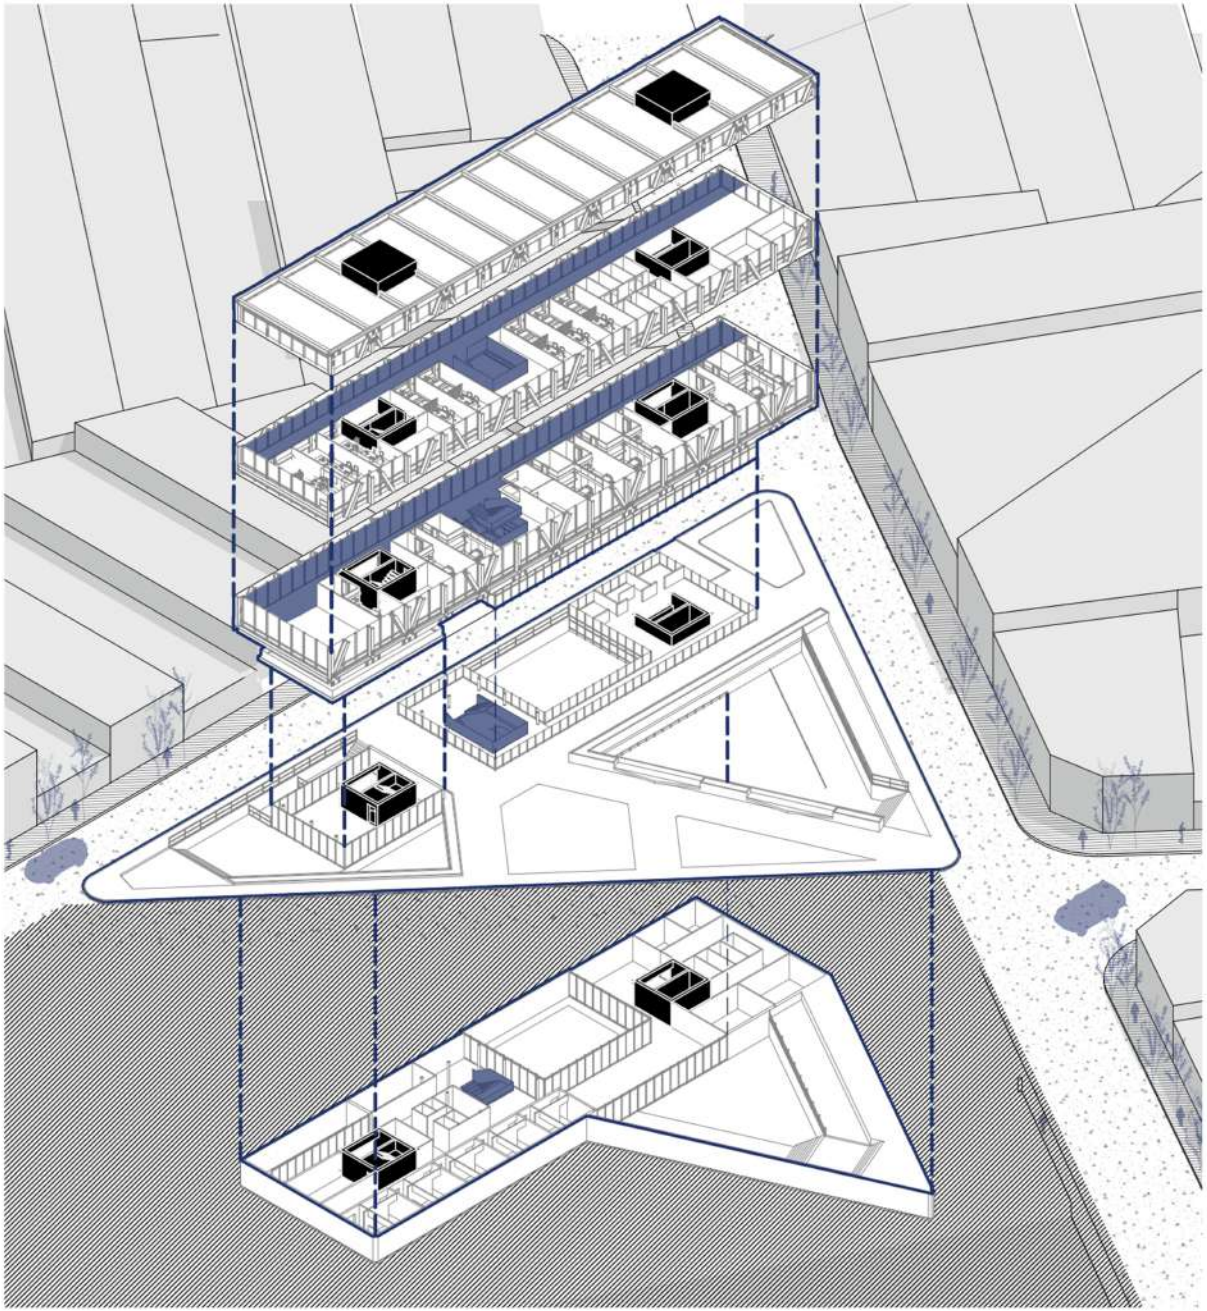


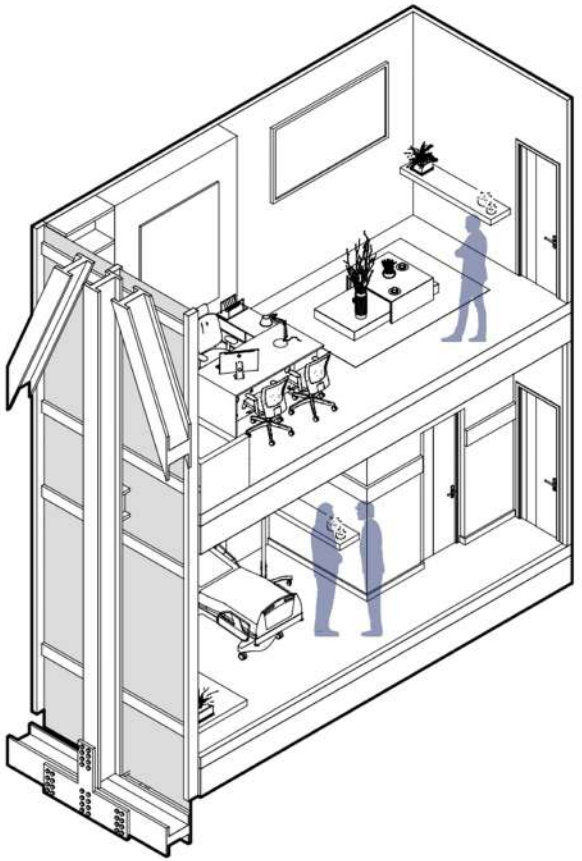


Cielorraso suspendido

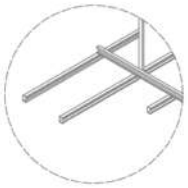

Curting wall

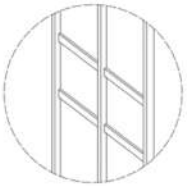

Estructura metalica perfiles IPN

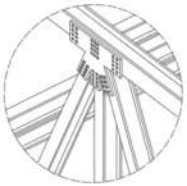




+ Enfermeria






MITOSIS TIGRE

A partir de la célula, la cual se pensó con la idea de crear espacios comunicados que se encuentren en distintos niveles, ofreciéndole al usuario la posibilidad de circular a través de estos y percibir el espacio desde distintas perspectivas. Utilizando figuras simples como los prismas se pudo realizar en la forma de encastrar estas generando espacialidades interiores que comunicaban las alturas de estas figuras.

Mediante este proyecto se pretende el aumento de la comunicación social entre vecinos y al mismo tiempo una mayor relación con el exterior proporcionando además numerosas vistas,


Una de las características de este proyecto son las terrazas de las que constan cada una de las viviendas, éstas están situadas sobre las cubiertas de los módulos inferiores, estas posibilitan a los usuarios su propio espacio libre. La composición de módulos escalonados además proporciona a cada vivienda acceso al sol y al aire.

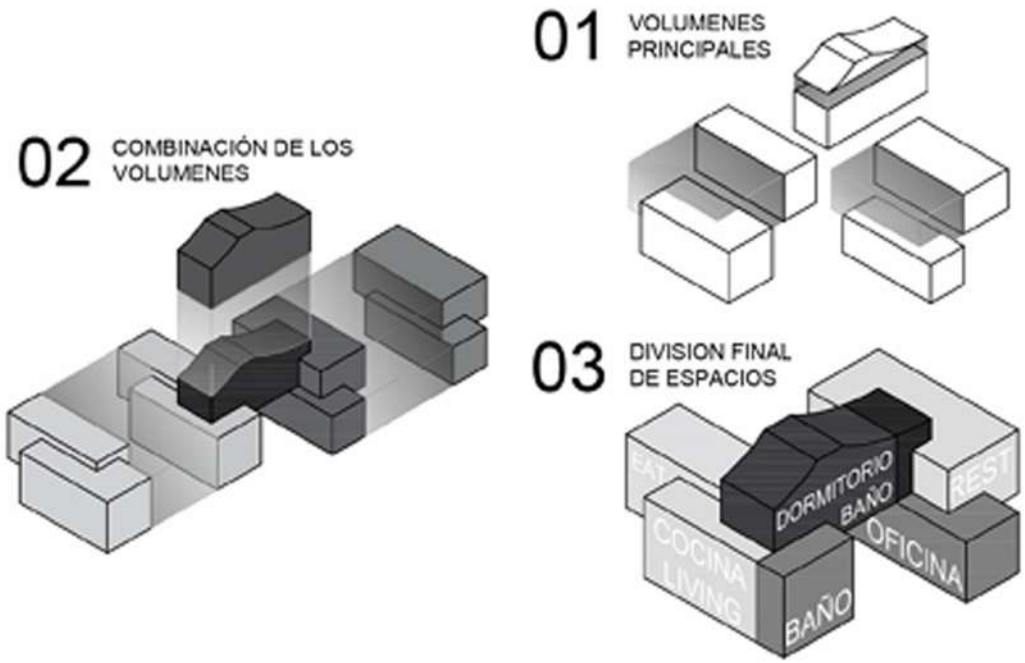





04 mitosis

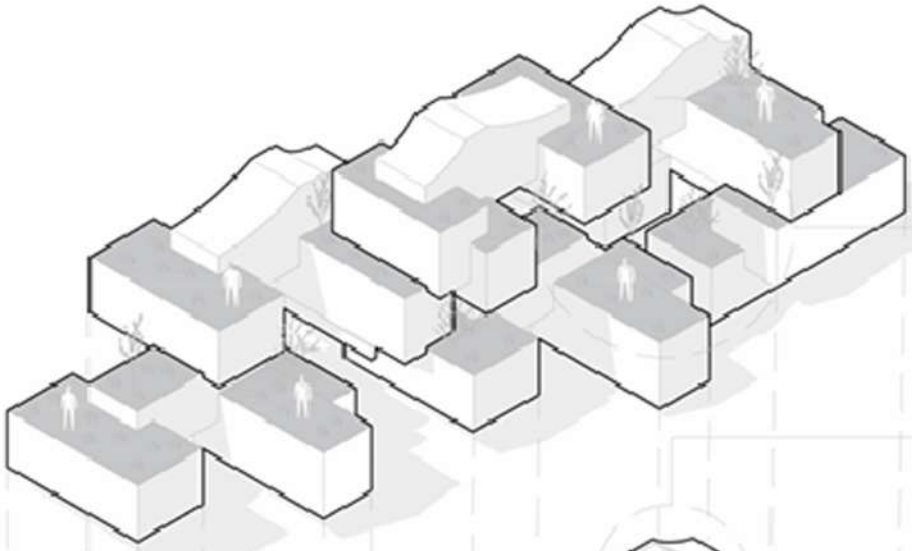


TERRAZAS Y SUSTENTABILIDAD

AL INTERCALAR Y ORIENTAR LAS DISTINTAS CELDAS, LOGRAMOS CREAR TERRAZAS INTERCONECTADAS Y NIVELADAS, QUE SON HABITABLES Y SUSTENTABLES, IDEALES PARA EL USO COTIDIANO DE LOS RESIDENTES DE NUESTRA OBRA.

TECHOS CURVADOS


ESTOS TECHOS, EN LAS ÚLTIMAS UNIDADES, NOS BRINDAN ESPACIOS MÁS AMPLIOS Y UNA CIRCULACIÓN DE AIRE, ASÍ COMO UNA ÓPTIMA UTILIZACIÓN DE LA LUZA NATURAL.

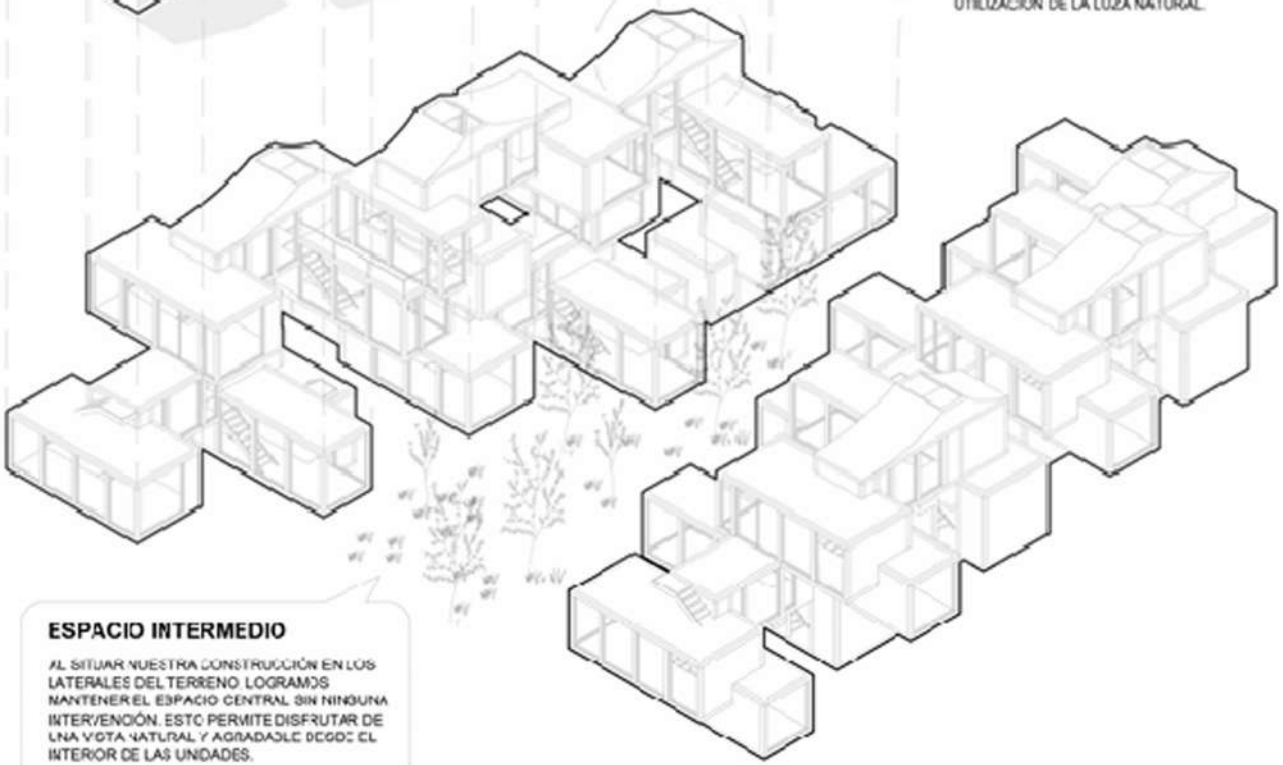


ESPACIO INTERMEDIO

AL SITUAR NUESTRA CONSTRUCCIÓN EN LOS LATERALES DEL TERRENO LOGRAMOS MANTENER EL ESPACIO CENTRAL SIN NINGUNA INTERVENCIÓN. ESTO PERMITE DISFRUTAR DE UNA VISTA NATURAL Y AGRADABLE DESDE EL INTERIOR DE LAS UNIDADES.


01 CELULAS BASES

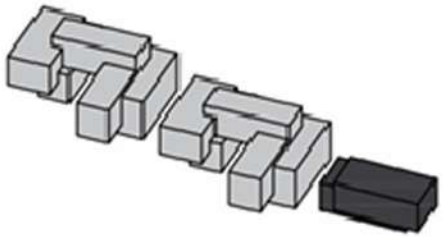


02 UNION

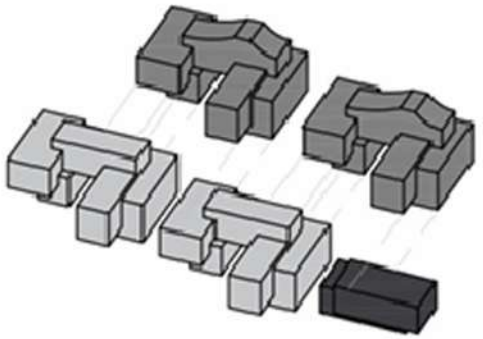

03 INTERSECCIÓN

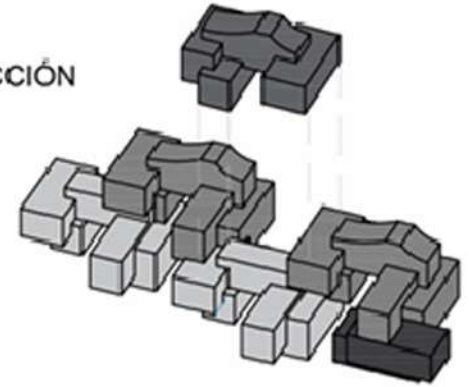

04 VOLUMETRIA DEL SECTOR

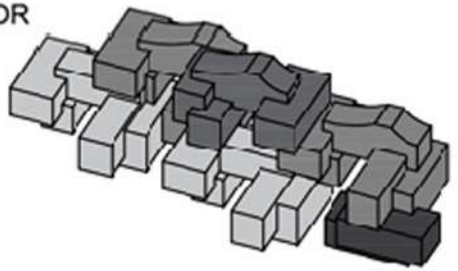










Este fue el modulo que se tomo para la repetición la cual prosederia a conformar la estructura y morfologia de esta obra, integrando asi la función de comunicar distintos niveles y terrazas. Lo interesante de esta conformación es el aprovechamiento que se le da a cada estacio de este modulo.






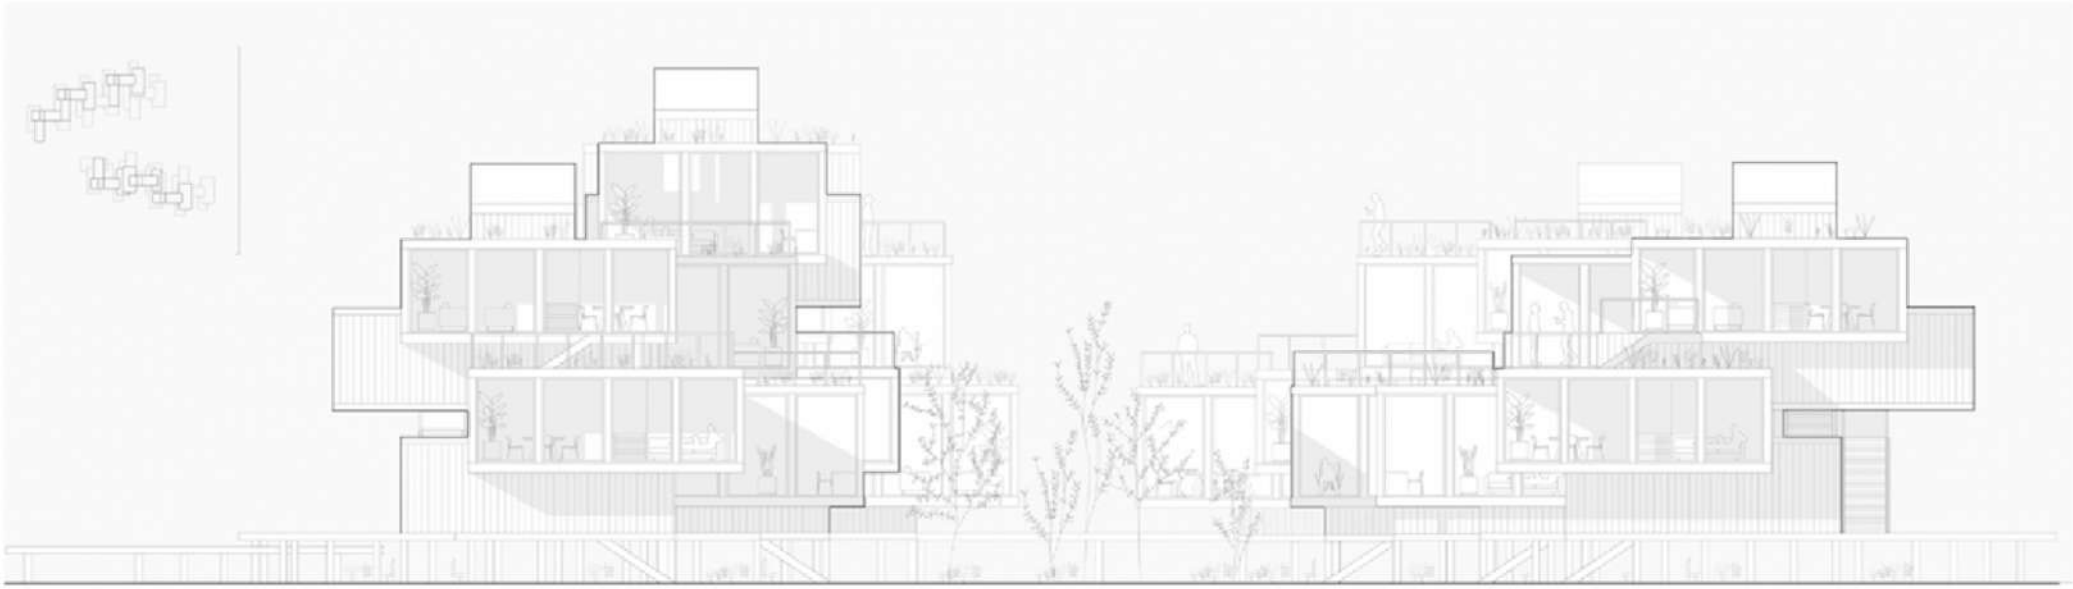






Vista - Corte en Detalle

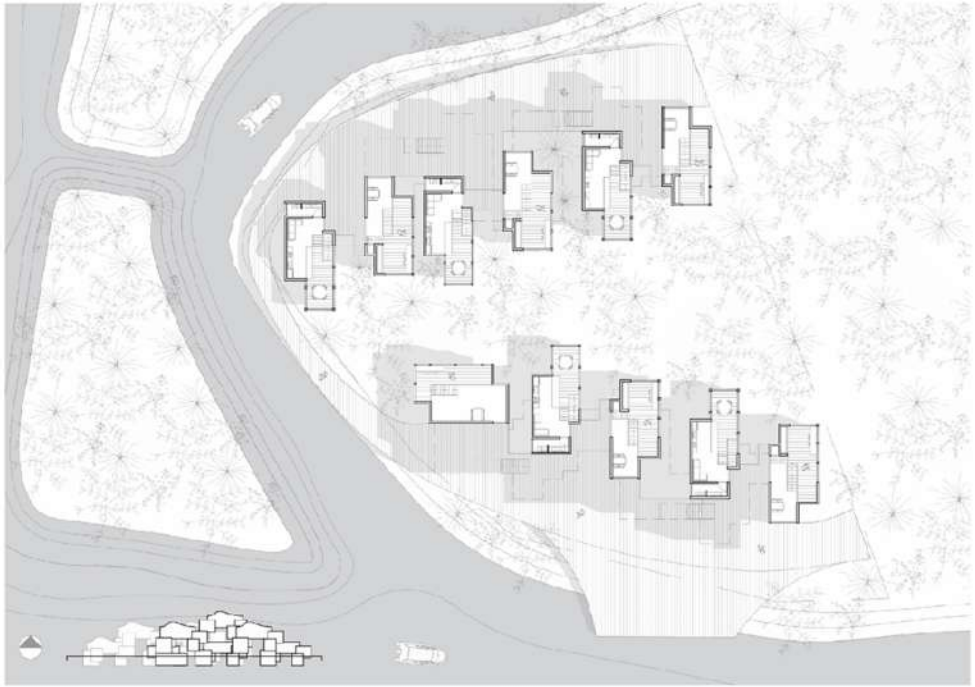

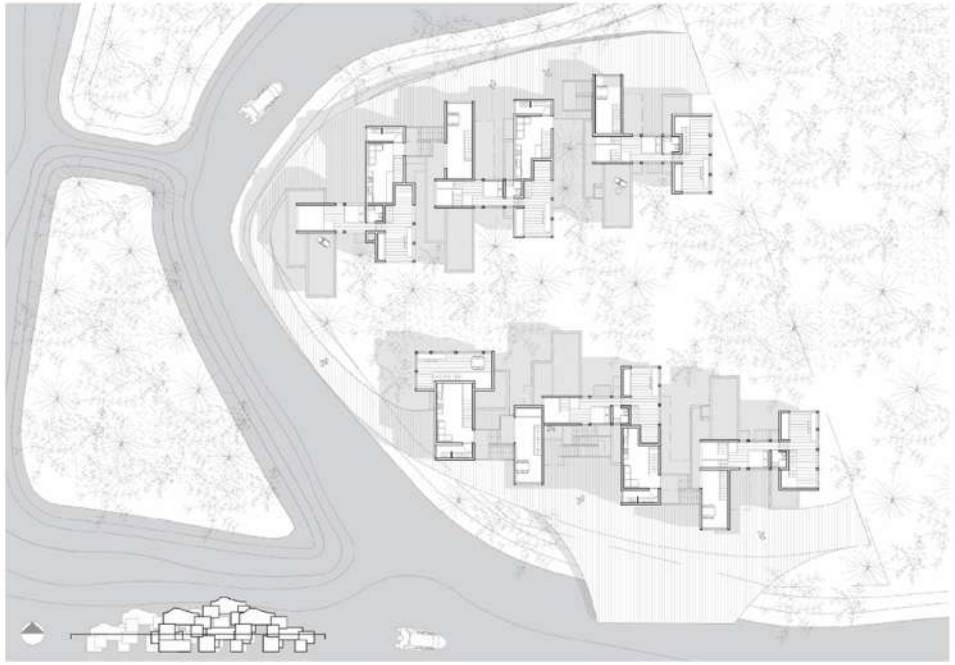


DOCUMENTACIÓN

Durante el último año de la secundaria, se nos encargó desarrollar un proyecto completo de un edificio a partir de una planta tipo, la cual fue modificada hasta convertirse en un diseño final.

A lo largo del proceso de planificación, abordamos temas como la medición según el código legal, lo cual nos permitió diferenciar los tipos de unidades que construiríamos, siempre respetando las normativas del terreno en el que trabajaríamos.

Desarrollamos los planos municipales, cortes y planos de replanteo necesarios para la construcción, además de calcular y diseñar la estructura general del edificio, incluyendo la diagramación y el diseño de la fachada.

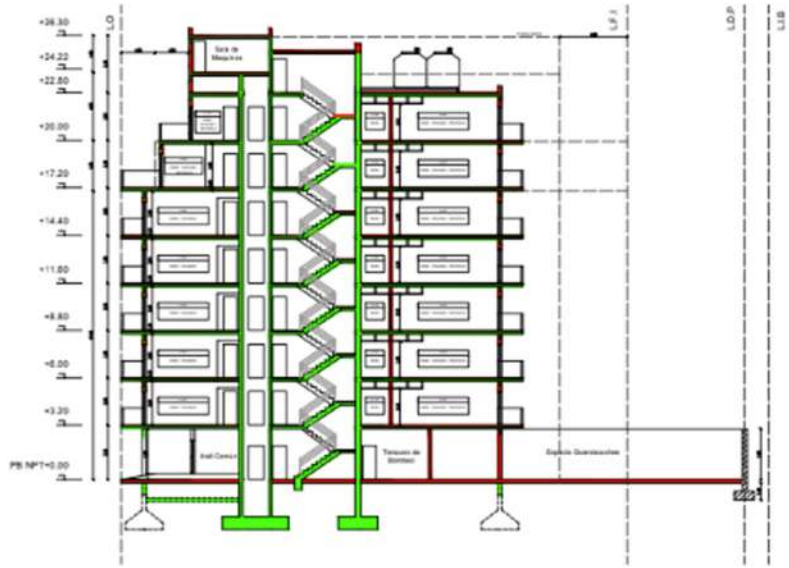



CORTE LONGITUDINAL




PLANILLA ILUMINACION Y VENTILACION




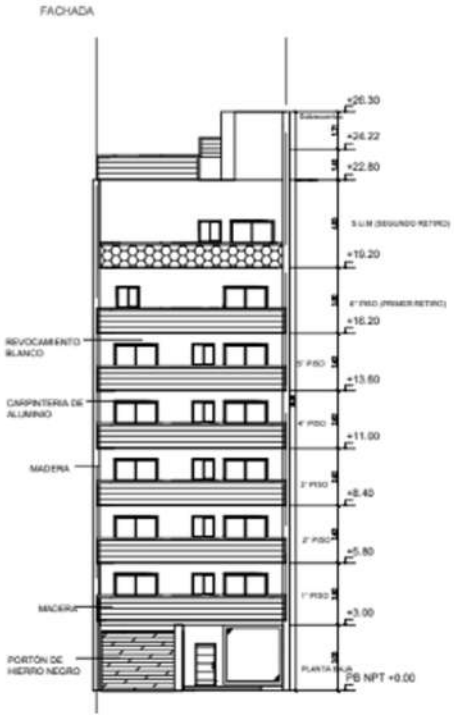

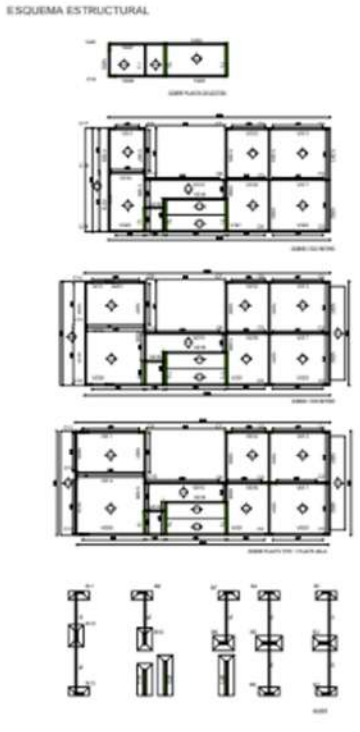

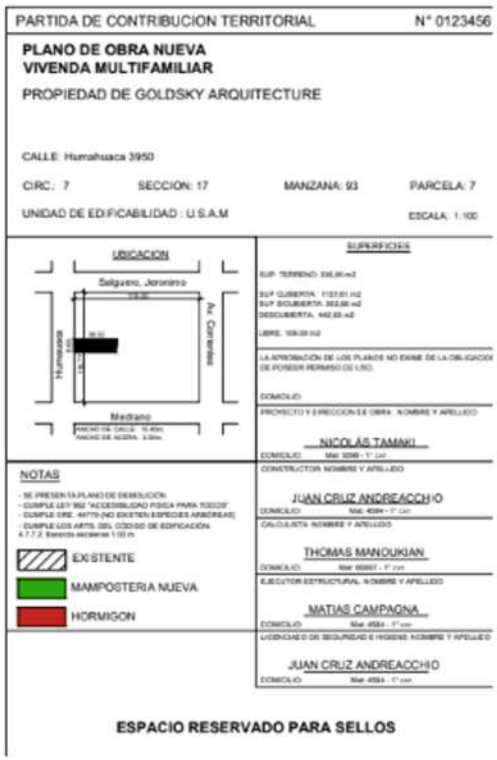


05 documentación

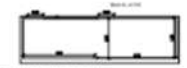

PLANTA DE TECHO




PLANTA AZOTEA

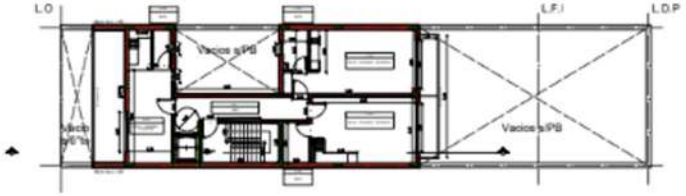


PLANTA 7° PISO




PLANTA 6° PISO

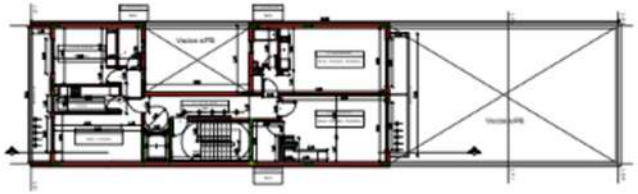


PLANTA TIPO 1° A 5° PISO

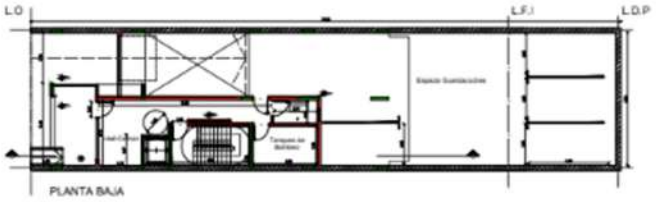


PLANTA BAJA

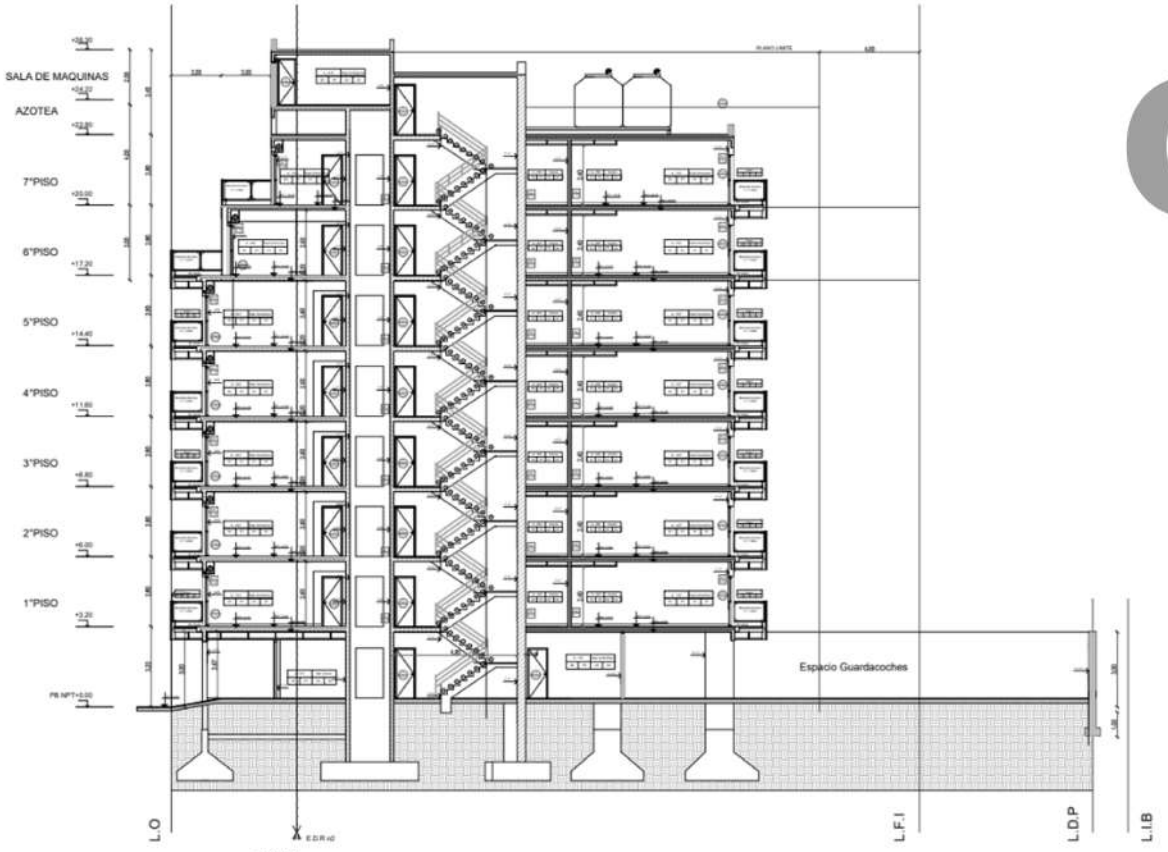

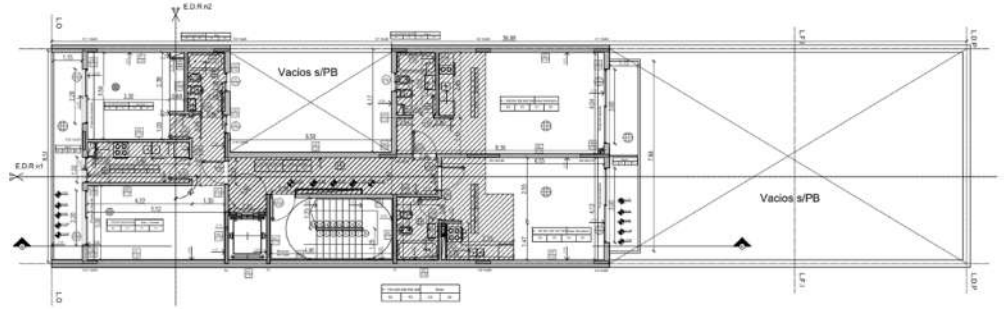

PLANTA TIPO 1° A 5° PISO

GoldSky Arquitecture	Obra: Vivienda Multifamiliar	Escala: 1:50
	Plano: Replanteo Planta Tipo	
Alumnos: Thomas Manoukian, Matias Campagna, Juan Cruz Andreacchio y Nicolas Tamaki		
Profesores: Sebastian Schilman/ Federico Ginzberg	Curso: 5° KE	Fecha: 29/11/2021

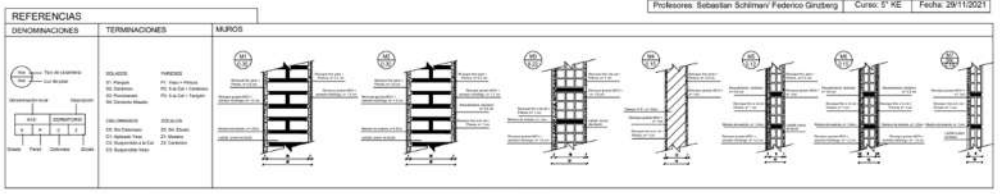

thomasmanoukian1118@gmail.com
+54 9 11 3872-3400